
SERVICE CORRIDOR
MAIN ENTRY
LOBBY / LAB
CENTRAL PLAZA
PEDESTRIAN BRIDGE
SERVICE ENTRY
LOADING AND DOCK SERVICE
PARKING GARAGE
PARKING GARAGE
PARKING GARAG


PARK DRIVE
PARK DRIVE
PARK DRIVE

ANNOTATION SYMBOLS



ENTRY

#18427E ICON + TRIANGLE



SERVICE / LOADING

#6C6C6C ICON + TRIANGLE



VIEW MARKER

#D8AE78, WHITE NUMBER, LEADER



PARKING / CAR

#6C6C6C TOP VIEW



PEDESTRIAN FLOW

#E47200 4 PT DASH



VEHICLE FLOW

#6C6C6C 4 PT DASH



VIEW / GATEWAY

#183C6C 2 PT DASH



TRANSIT STOP

#2F6DB5 ICON

TREE

CANOPY CIRCLE (PLAN) / LOLLIPOP (AXON)



TAG

ROUNDED LABEL + LEADER

FUTURE BLDG

FUTURE BUILDING

CONTEXT LABEL: PD CONTEXT LABEL STYLE

MAIN ST

STREET NAME


PD NOTE CAPS, ROTATED ALONG THE STREET

NOTE


NOTE / ANNOTATION

PD NOTE

L1M

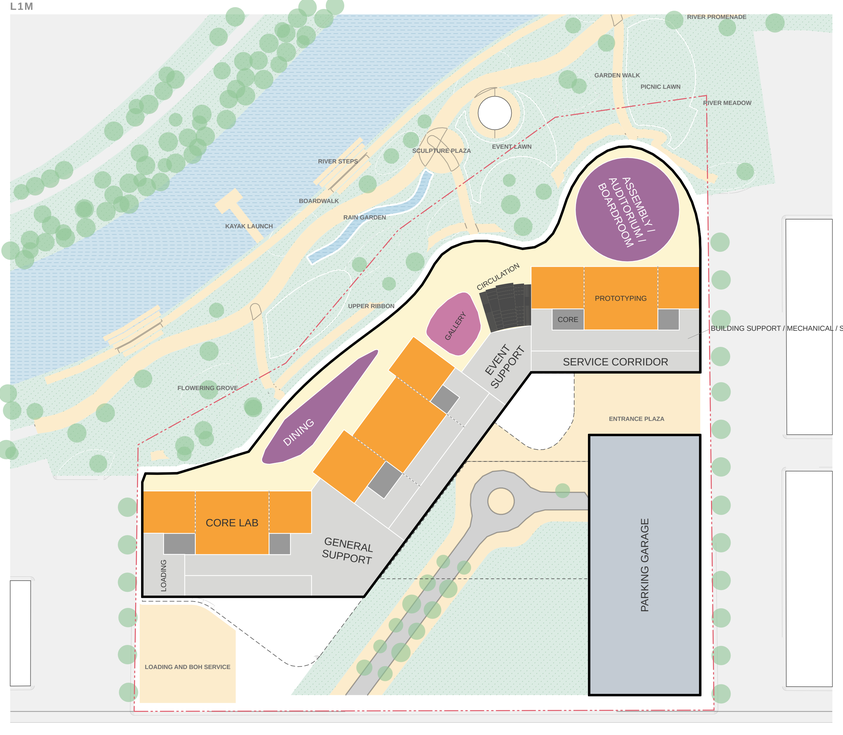
RIVER PROMENADE
GARDEN WALK
PICNIC LAWN
RIVER MEADOW
RIVER STEPS
SCULPTURE PLAZA
EVENT LAWN
BOARDWALK
RAIN GARDEN
KAYAK LAUNCH
ASSEMBLY / AUDITORIUM / BOARDROOM
CIRCULATION
PROTOTYPING
CORE
UPPER RIBBON
GALLERY
EVENT SUPPORT
SERVICE CORRIDOR
BUILDING SUPPORT / MECHANICAL / STORAGE
FLOWERING GROVE
DINING
ENTRANCE PLAZA
CORE LAB
GENERAL SUPPORT
LOADING
PARKING GARAGE
LOADING AND BOH SERVICE


L2

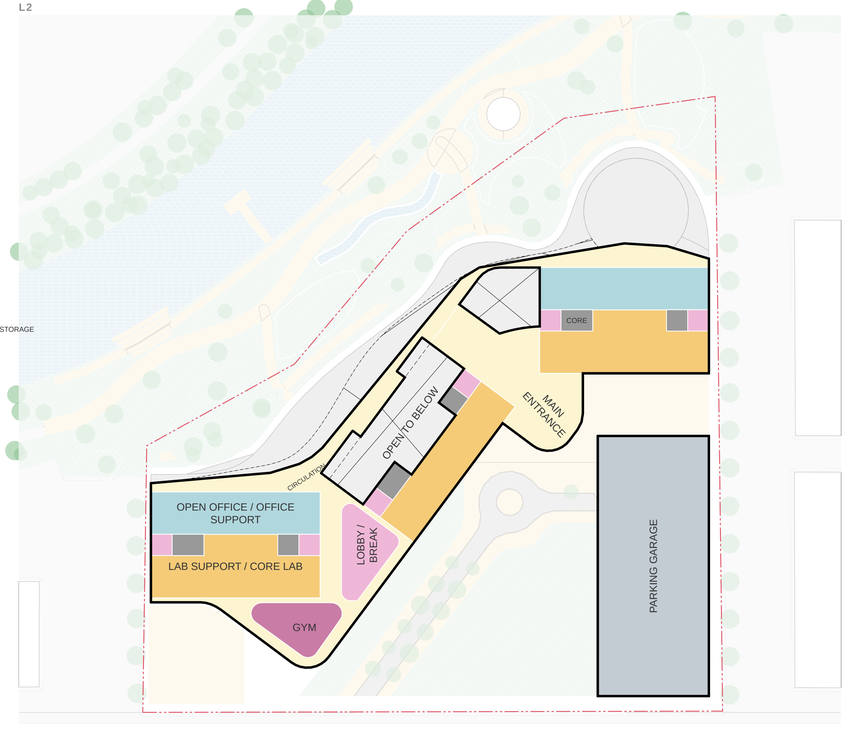
CORE
OPEN TO BELOW
MAIN ENTRANCE
CIRCULATION
OPEN OFFICE / OFFICE SUPPORT
LOBBY / BREAK
LAB SUPPORT / CORE LAB
GYM
PARKING GARAGE

L3


LOBBY / BREAK
EXECUTIVE OFFICE
CORE
OPEN OFFICE / OFFICE SUPPORT
CIRCULATION
OFFICE
LAB SUPPORT / CORE LAB
PARKING GARAGE

L4

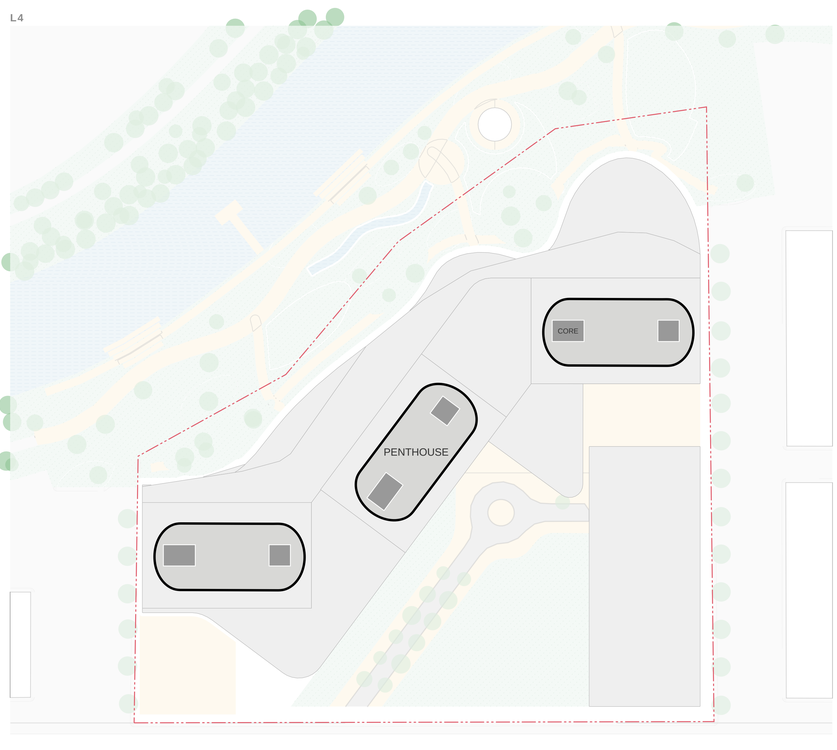
CORE
PENTHOUSE

SCALE 1/64" = 1'-0"
0 200'
N

RIVER PROMENADE
GARDEN WALK
PICNIC LAWN
RIVER MEADOW
SCULPTURE PLAZA
EVENT LAWN
RIVER STEPS
BOARDWALK
RAIN GARDEN
KAYAK LAUNCH
UPPER RIBBON
FLOWERING GROVE
ASSEMBLY / AUDITORIUM / BOARDROOM
CIRCULATION
PROTOTYPING
CORE
GALLERY
BUILDING SUPPORT / MECHANICAL / STORAGE
EVENT SUPPORT
SERVICE CORRIDOR
ENTRANCE PLAZA
DINING
CORE LAB
GENERAL SUPPORT
LOADING
PARKING GARAGE
LOADING AND BOH SERVICE

LAB
CONFERENCE
PARKING
CIRCULATION
ASSEMBLY / AUDITORIUM / BOARDROOM
BUILDING SUPPORT / MECHANICAL / STORAGE
CORE

L1M

SCALE 1/64" = 1'-0"

0 200'

N

CORE

MAIN ENTRANCE

OPEN TO BELOW

CIRCULATION

OPEN OFFICE / OFFICE SUPPORT

LAB SUPPORT / CORE LAB

LOBBY / BREAK

GYM

PARKING GARAGE

OPEN OFFICE / OFFICE SUPPORT
CONFERENCE
PARKING
LAB SUPPORT / CORE LAB
LOBBY / BREAK
CIRCULATION
CORE

LEVEL 2

SCALE 1/64" = 1'-0"

0 200'

N

EXECUTIVE OFFICE

LOBBY / BREAK

CORE

OPEN OFFICE / OFFICE SUPPORT

CIRCULATION

OFFICE

LAB SUPPORT / CORE LAB

PARKING GARAGE

OFFICE
CIRCULATION
PARKING
OPEN OFFICE / OFFICE SUPPORT
LOBBY / BREAK
LAB SUPPORT / CORE LAB
CORE

LEVEL 3

SCALE 1/64" = 1'-0"

0 200'

N

CORE

PENTHOUSE

BUILDING SUPPORT / MECHANICAL / STORAGE

CORE

LEVEL 4

PROGRAM

- OFFICE
- OPEN OFFICE / OFFICE SUPPORT
- LAB
- LAB SUPPORT / CORE LAB
- CIRCULATION
- BUILDING SUPPORT / MECHANICAL / STORAGE
- VIVARIUM
- VIVARIUM SUPPORT
- VIVARIUM PROCEDURE
- CONFERENCE
- LOBBY / BREAK
- INTERACTION / COLLAB
- ASSEMBLY / AUDITORIUM / BOARDROOM
- CLINIC
- CLINIC SUPPORT
- GREEN ROOF / SKY GARDEN
- CORE
- STAIR / TRANSPORTATION
- SHELL / PENTHOUSE
- VOID
- UNASSIGNED
- PARKING

SITE / CONTEXT / NC

- NC.SCREEN
- NC.STRUCTURE
- NC.ROOF
- NC.GREEN
- NC.HARDSCAPE
- NC.TREE
- NC.WATER
- NC.INTERIOR
- NC.FURNITURE
- NC.MASSING
- NC.PROPERTYLINE
- BG.BUILDING
- BG.ROAD
- BG.HARDSCAPE
- BG.LANDSCAPE
- BG.TREE
- BG.WATER
- BG.LINE
- ENTOURAGE

LINES

- BUILDING OUTLINE
- ROOM DIVIDER
- GLASS LINE
- OPEN TO BELOW
- LEADER
- HARDSCAPE EDGE
- SITE / ROAD EDGE

ANNOTATION

N SCALE 1/64" = 1'-0"

0 100'


LEVEL 1

ANNOTATION SYMBOLS

- ENTRY — #18427E ICON + TRIANGLE
- SERVICE / LOADING — #6C6C6C ICON + TRIANGLE
- VIEW MARKER — #D8AE78, WHITE NUMBER, LEADER
- PARKING / CAR — #6C6C6C TOP VIEW
- PEDESTRIAN FLOW — #E47200 4 PT DASH
- VEHICLE FLOW — #6C6C6C 4 PT DASH
- VIEW / GATEWAY — #183C6C 2 PT DASH
- TRANSIT STOP — #2F6DB5 ICON
- TREE — CANOPY CIRCLE (PLAN) / LOLLIPOP (AXON)
- TAG — ROUNDED LABEL + LEADER
- FUTURE BLDG — FUTURE BUILDING — CONTEXT LABEL: PD CONTEXT LABEL STYLE
- MAIN ST — STREET NAME — PD NOTE CAPS, ROTATED ALONG THE STREET
- NOTE — NOTE / ANNOTATION — PD NOTE


ENTOURAGE



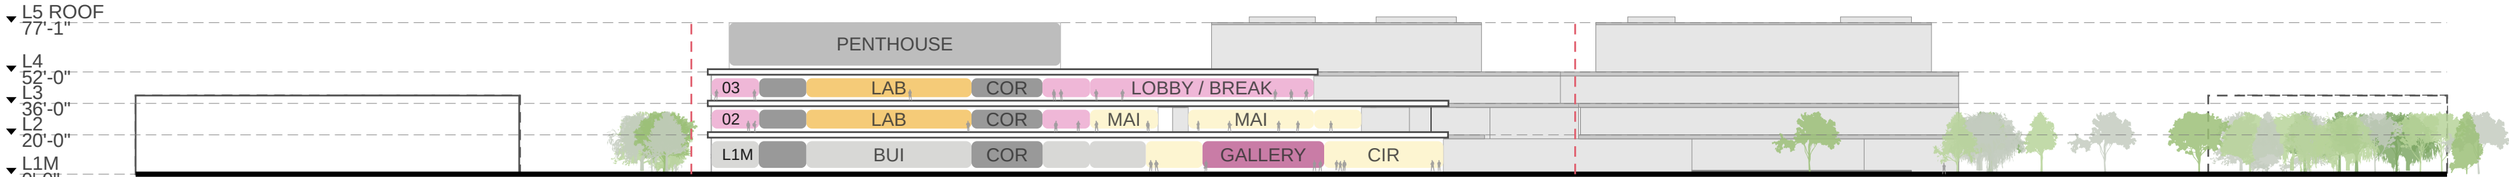


SECTION A

SCALE 1/64" = 1'-0"

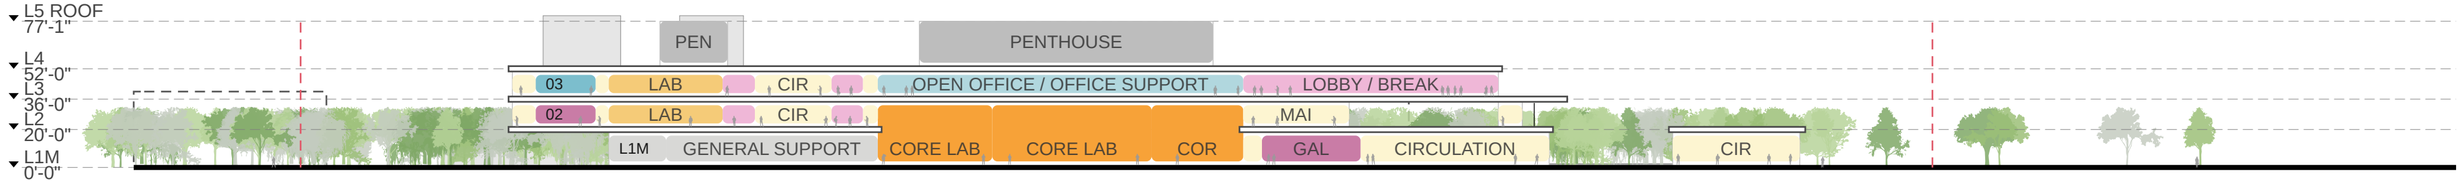

SECTION B

SCALE 1/64" = 1'-0"

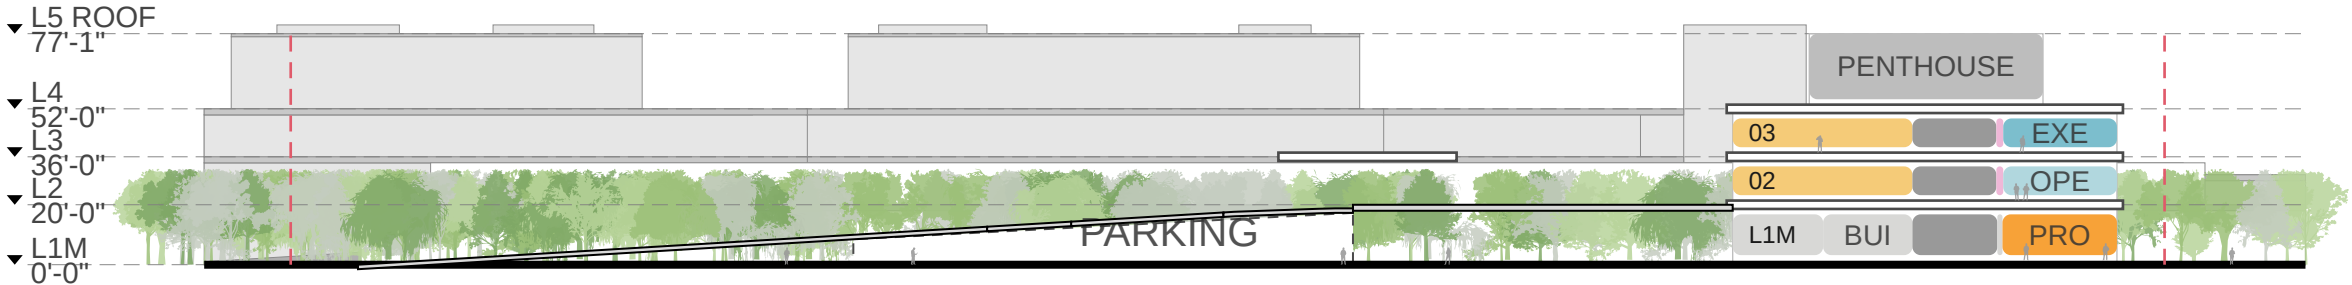


SECTION C

SCALE 1/64" = 1'-0"



SECTION D

SCALE 1/64" = 1'-0"

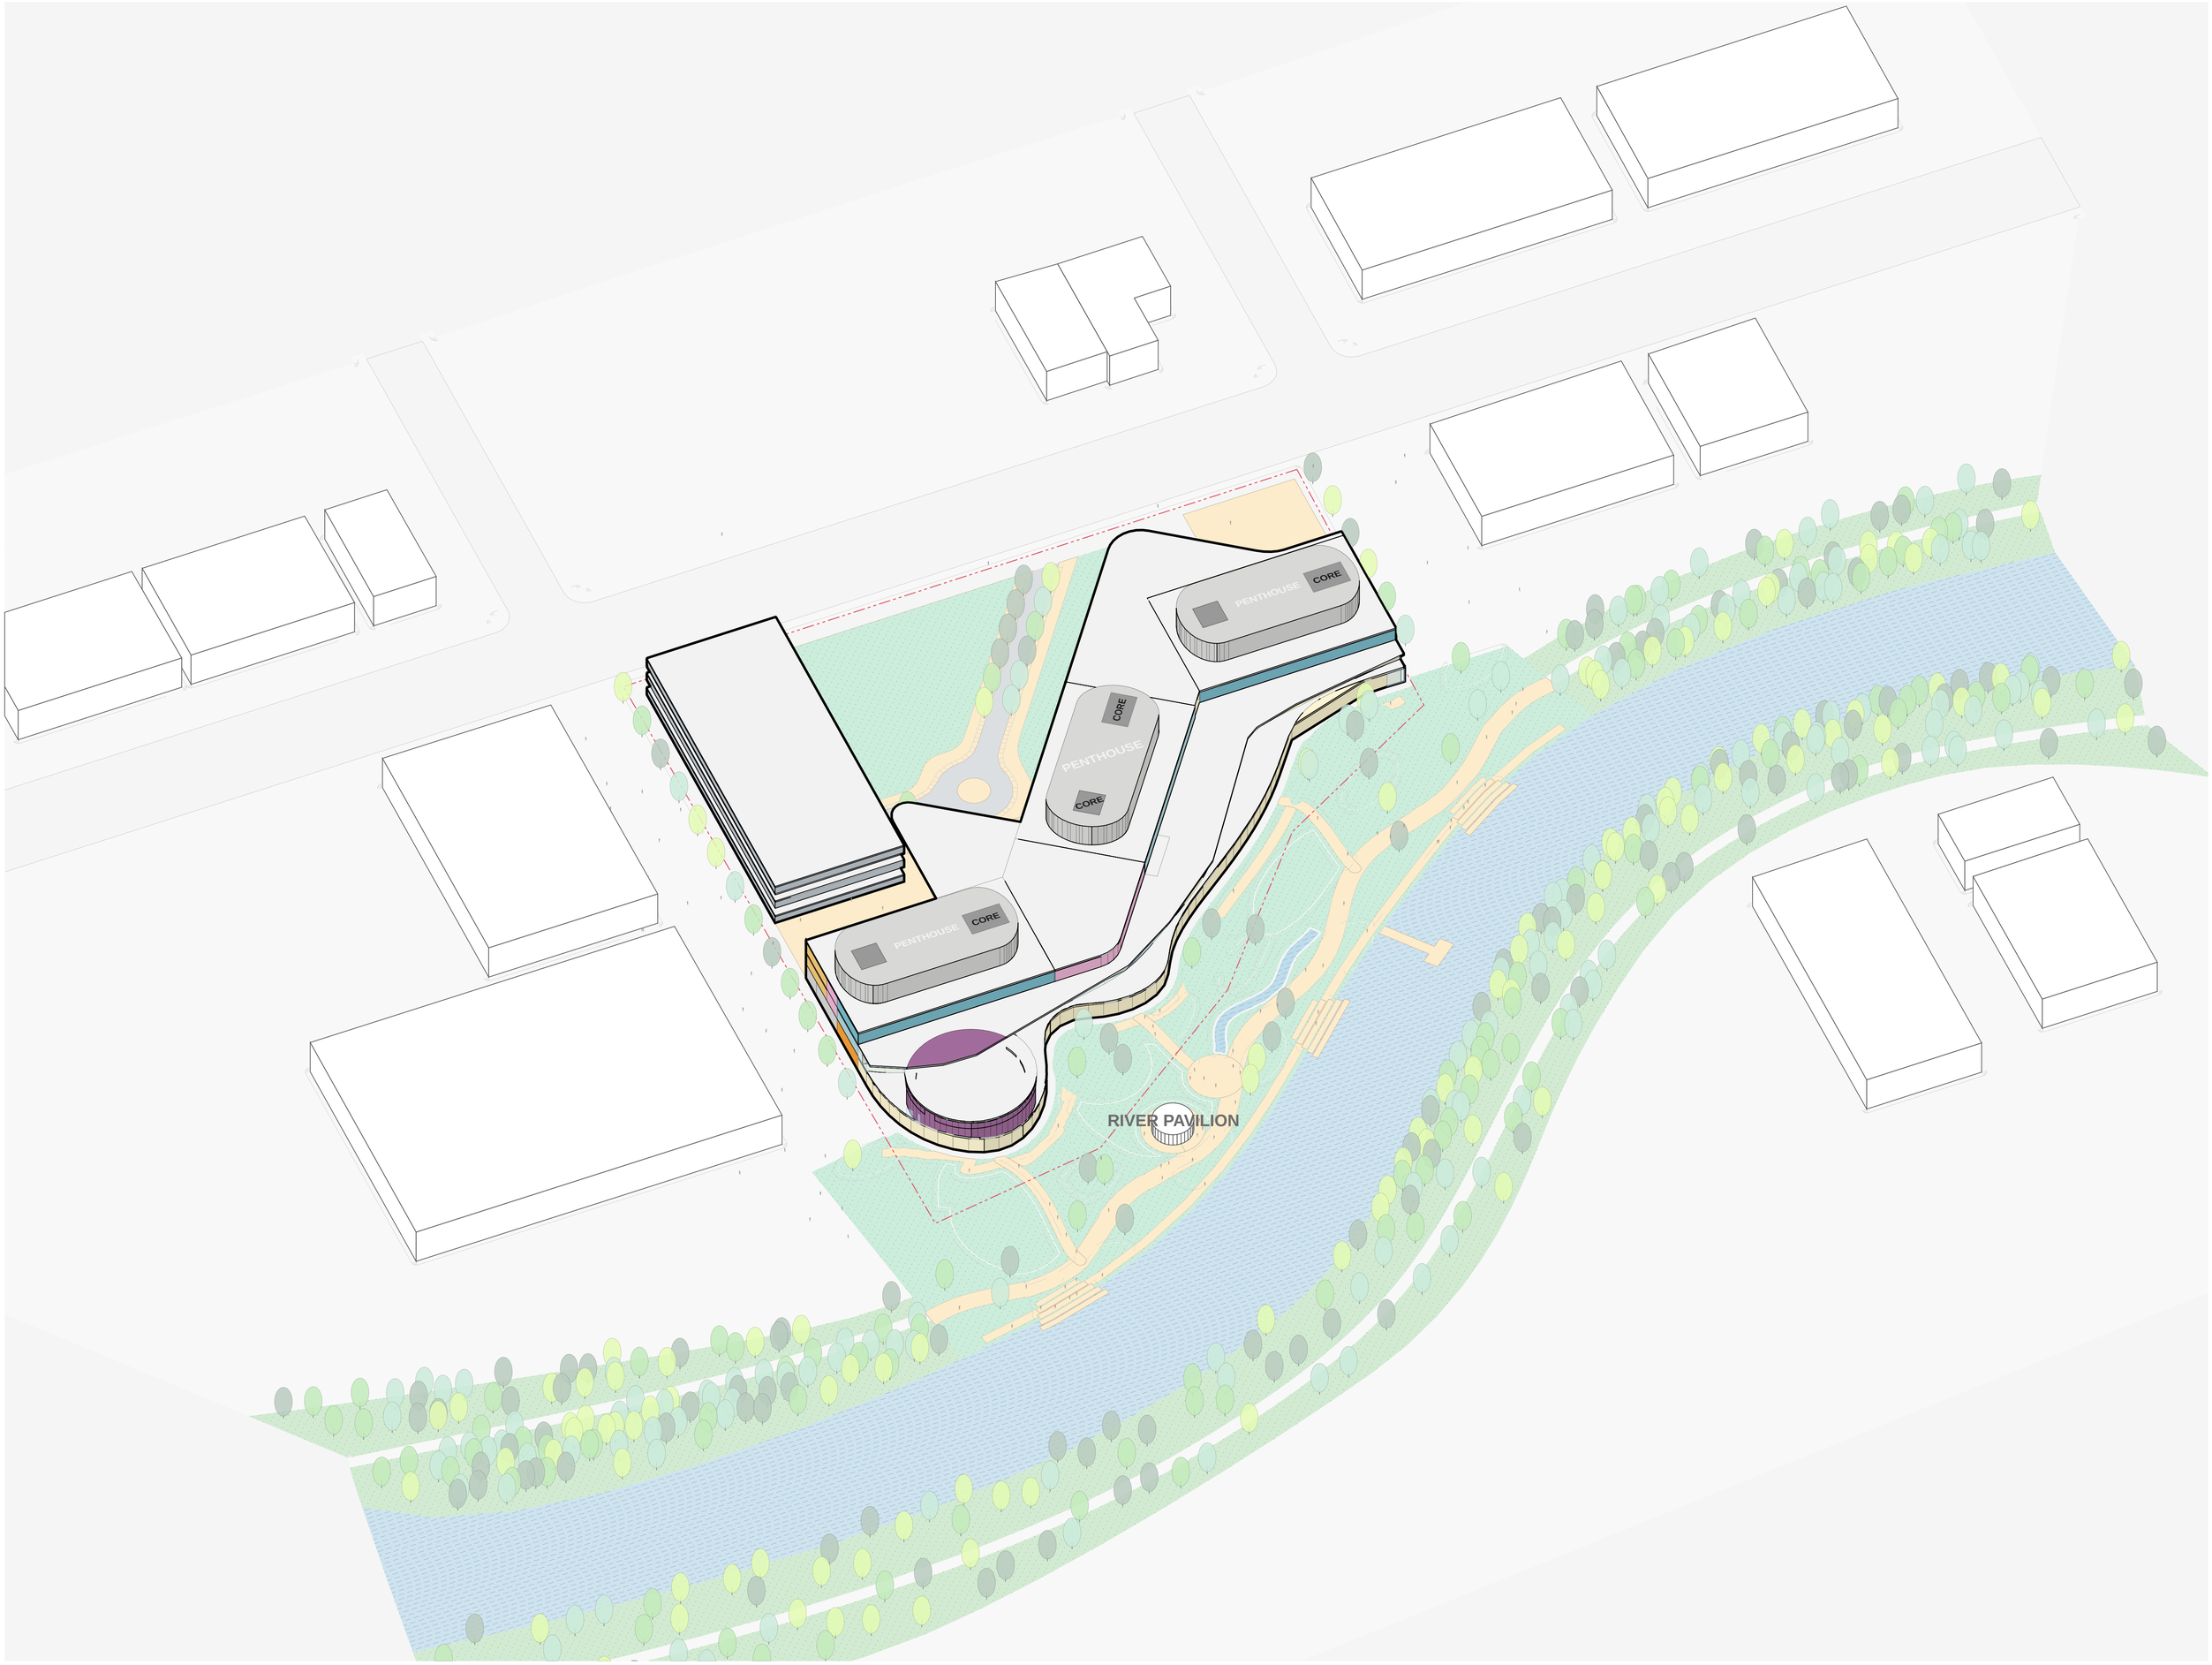

SITE AXON

SCALE 1/64" = 1'-0"

N

AXON LEGEND



TAG
ROUNDED LABEL + LEADER



PEDESTRIAN FLOW
#E47200 4 PT DASH



VEHICLE FLOW
#6C6C6C 4 PT DASH



TRANSIT STOP
#2F6DB5 ICON



VIEW / GATEWAY
#183C6C 2 PT DASH



SERVICE / LOADING
#6C6C6C ICON + TRIANGLE



ENTRY
#18427E ICON + TRIANGLE



VIEW MARKER
#D8AE78, WHITE NUMBER, LEADER

TREE
CANOPY CIRCLE (PLAN) / LOLLIPOP (AXON)

FUTURE BLDG


FUTURE BUILDING
CONTEXT LABEL: PD CONTEXT LABEL STYLE

MAIN ST

STREET NAME
PD NOTE CAPS, ROTATED ALONG THE STREET

NOTE

NOTE / ANNOTATION
PD NOTE

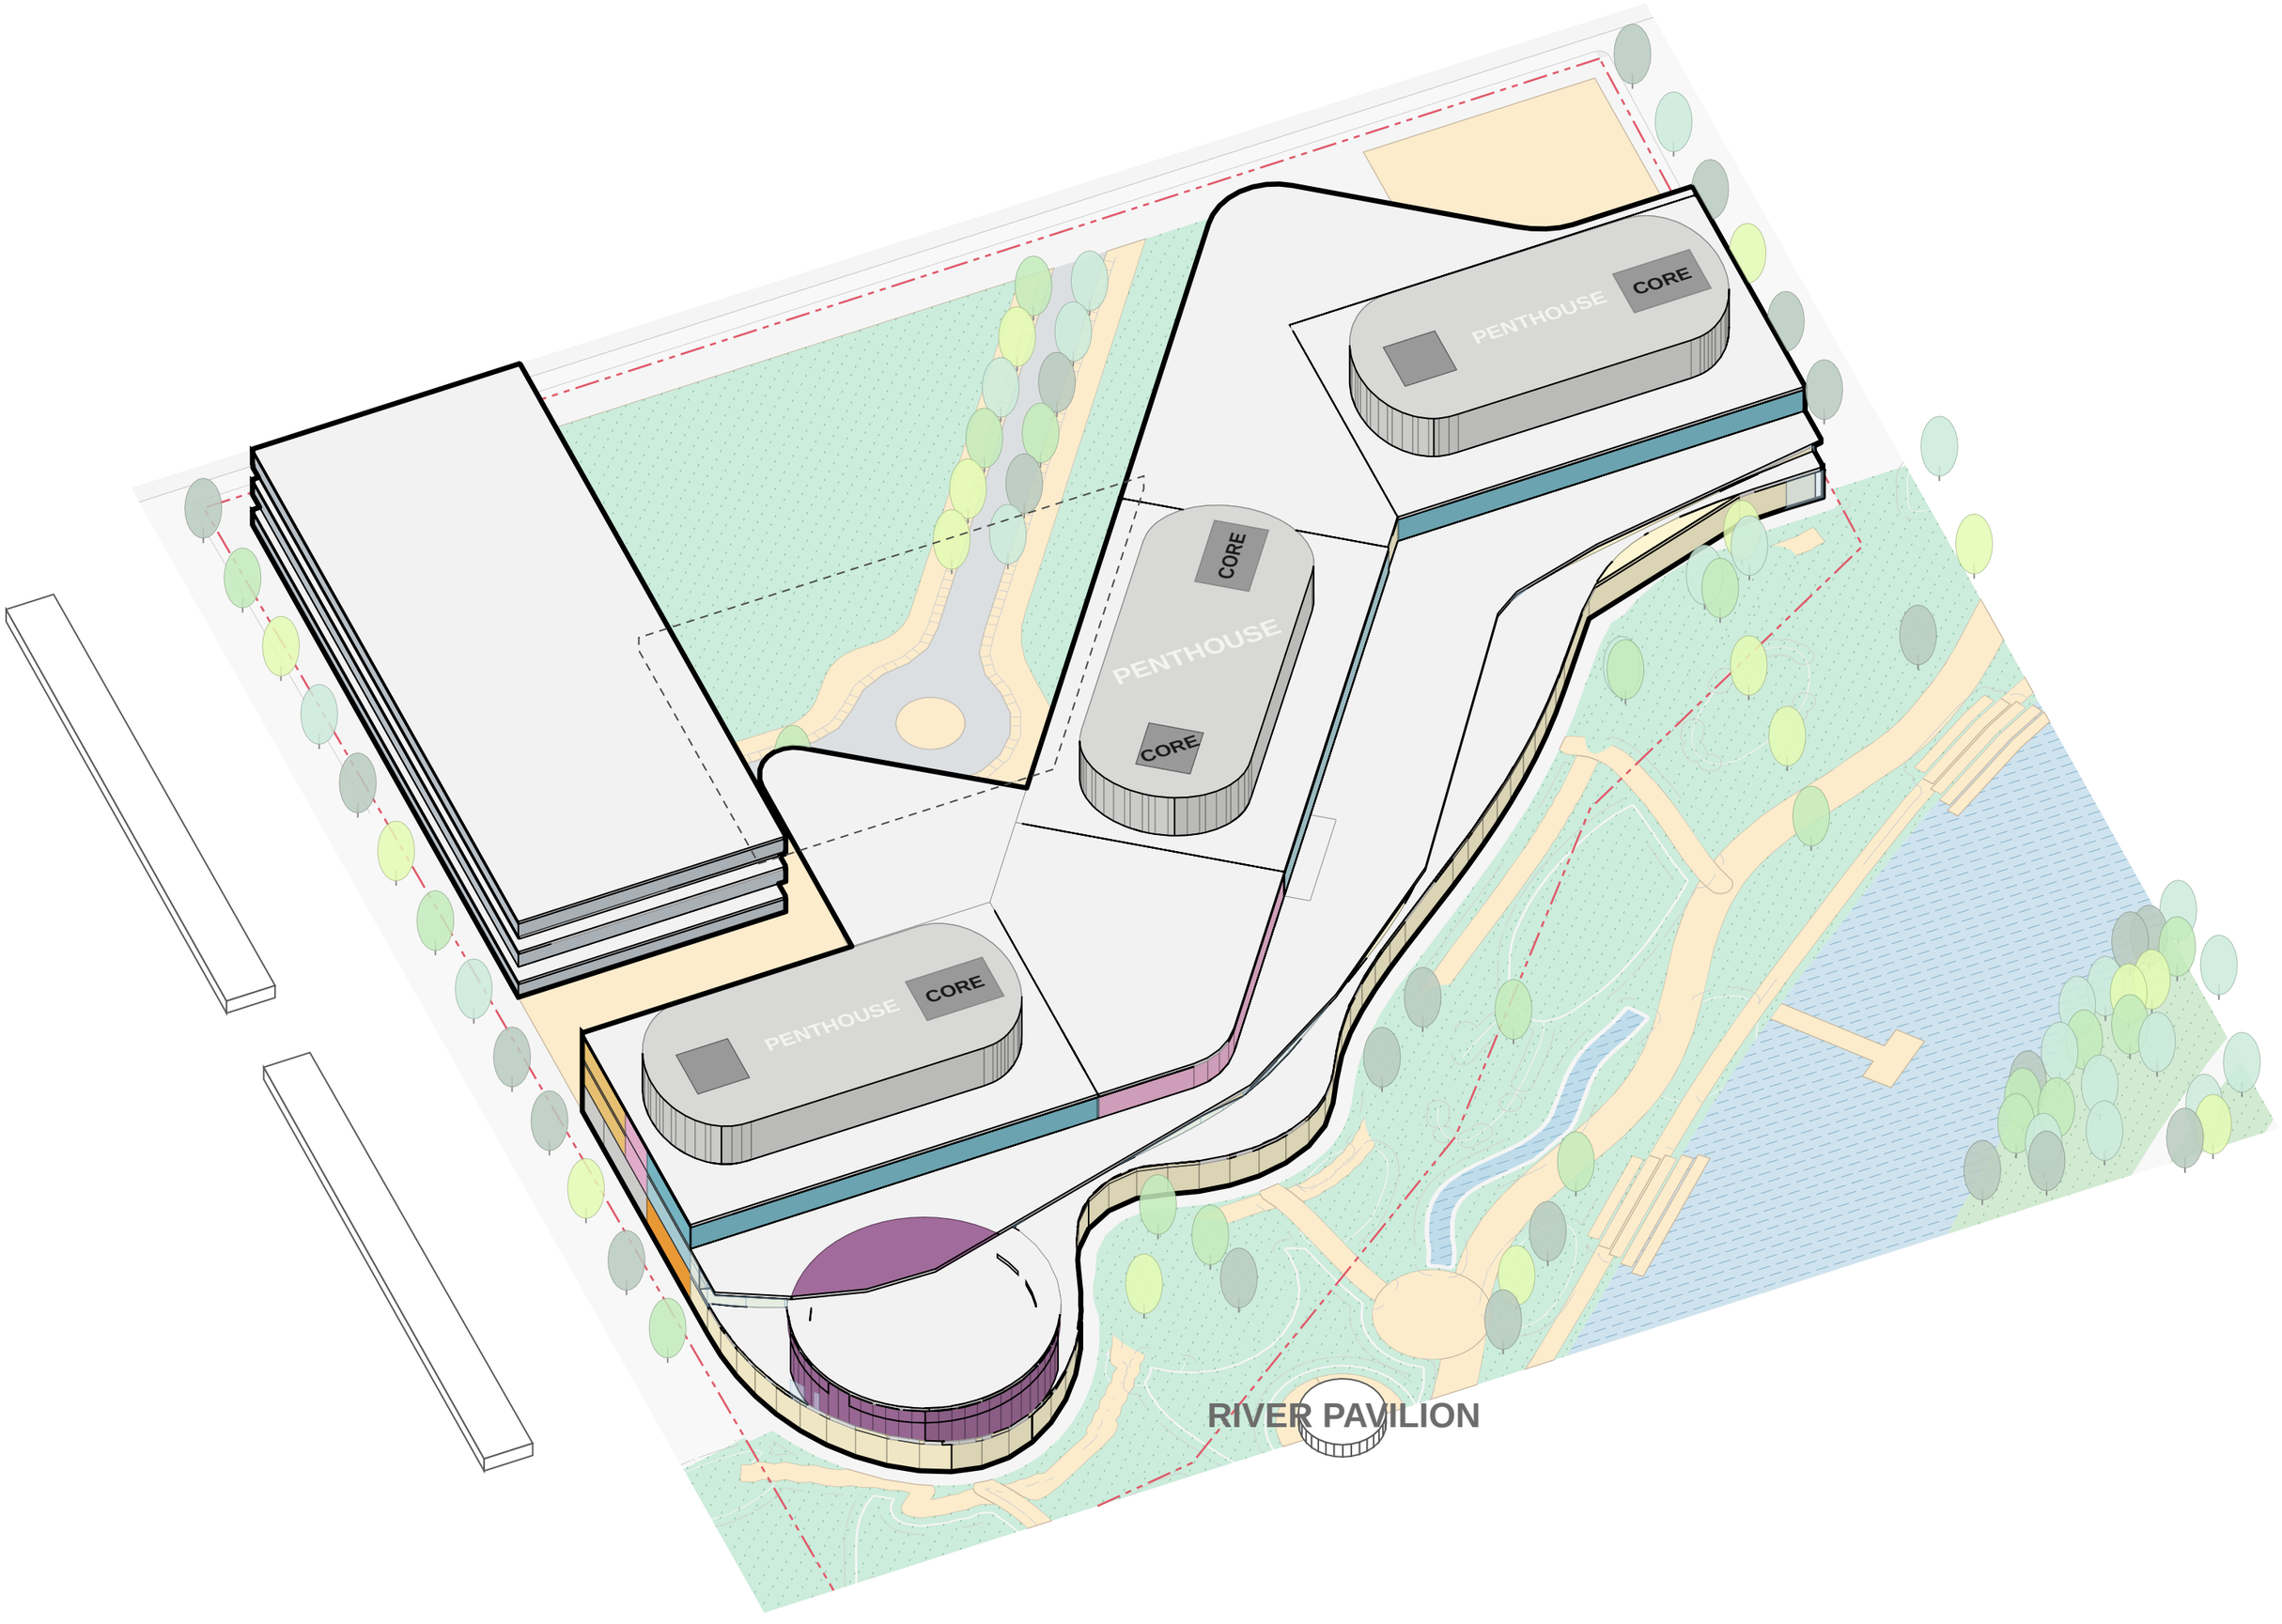

STACKED AXON

SCALE 1/64" = 1'-0"

N

AXON LEGEND



TAG
ROUNDED LABEL + LEADER



PEDESTRIAN FLOW
#E47200 4 PT DASH



VEHICLE FLOW
#6C6C6C 4 PT DASH



TRANSIT STOP
#2F6DB5 ICON



VIEW / GATEWAY
#183C6C 2 PT DASH



SERVICE / LOADING
#6C6C6C ICON + TRIANGLE



ENTRY
#18427E ICON + TRIANGLE



VIEW MARKER
#D8AE78, WHITE NUMBER, LEADER

TREE
CANOPY CIRCLE (PLAN) / LOLLIPOP (AXON)

FUTURE BLDG


FUTURE BUILDING
CONTEXT LABEL: PD CONTEXT LABEL STYLE

MAIN ST

STREET NAME
PD NOTE CAPS, ROTATED ALONG THE STREET

NOTE

NOTE / ANNOTATION
PD NOTE

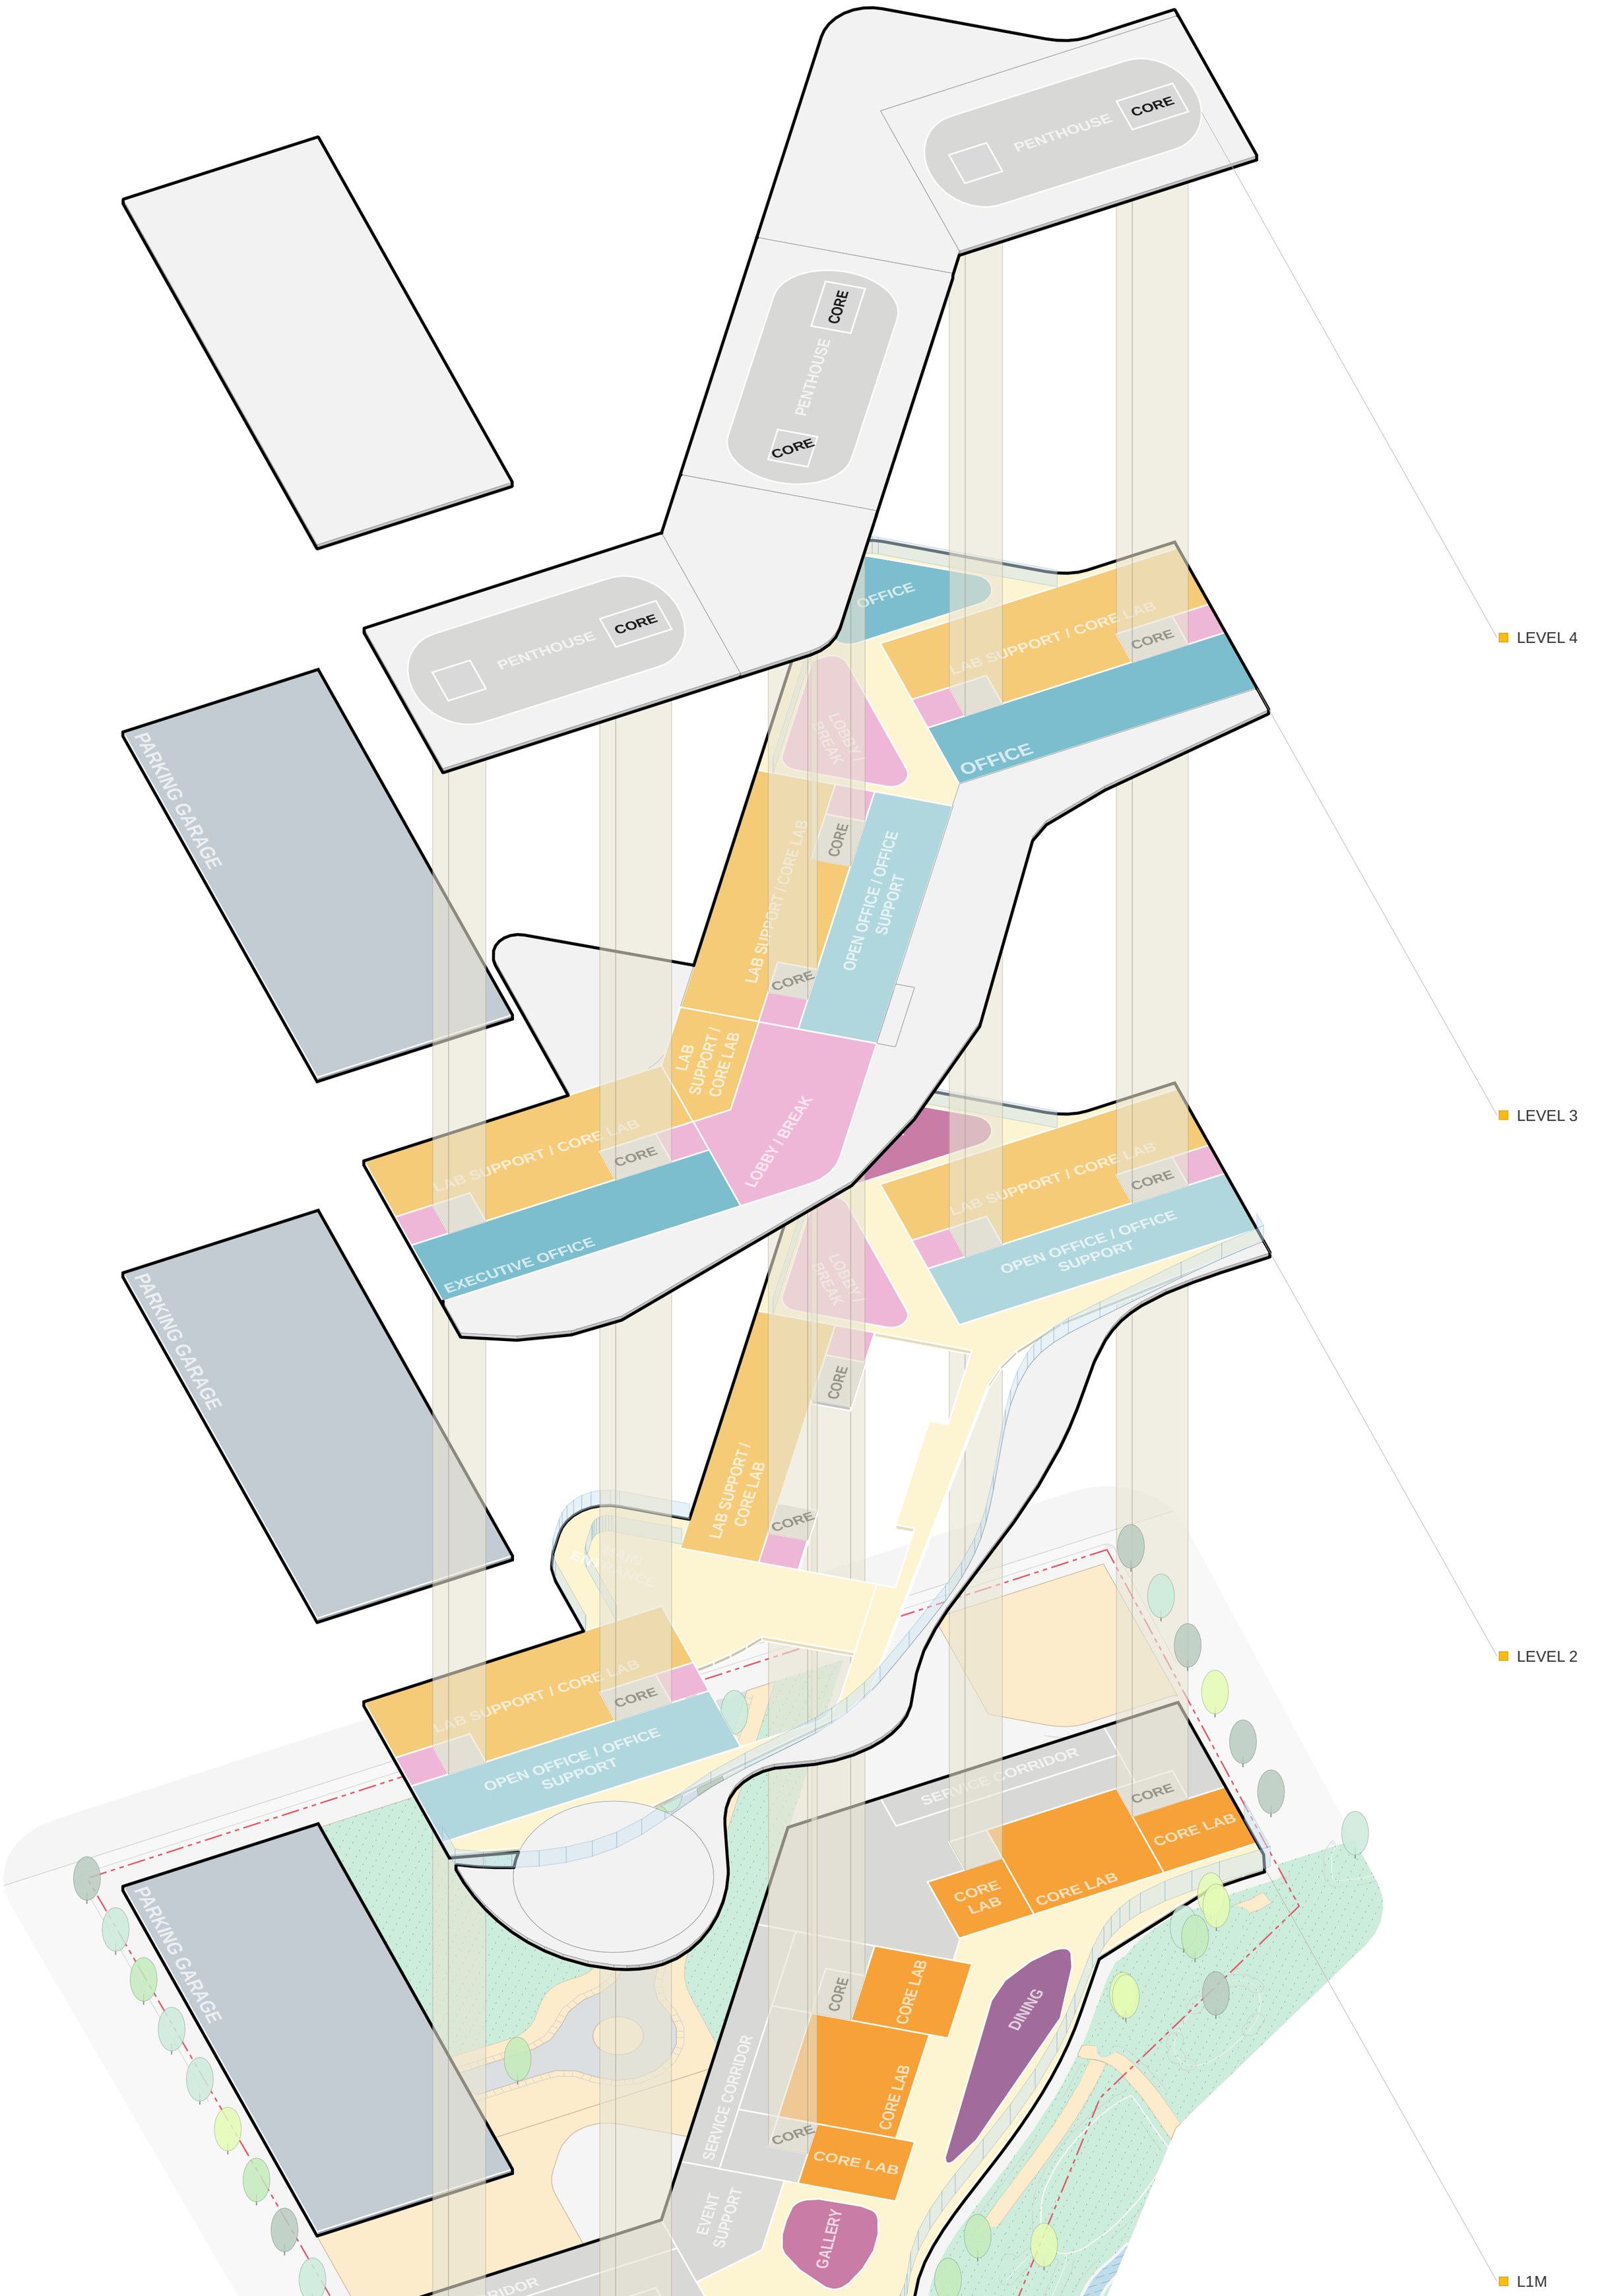

EXPLODED AXON

SCALE 1/64" = 1'-0"

N

AXON LEGEND



TAG
ROUNDED LABEL + LEADER



PEDESTRIAN FLOW
#E47200 4 PT DASH



VEHICLE FLOW
#6C6C6C 4 PT DASH



TRANSIT STOP
#2F6DB5 ICON



VIEW / GATEWAY
#183C6C 2 PT DASH



SERVICE / LOADING
#6C6C6C ICON + TRIANGLE



ENTRY
#18427E ICON + TRIANGLE



VIEW MARKER
#D8AE78, WHITE NUMBER, LEADER

TREE
CANOPY CIRCLE (PLAN) / LOLLIPOP (AXON)

FUTURE BLDG


FUTURE BUILDING
CONTEXT LABEL: PD CONTEXT LABEL STYLE

MAIN ST

STREET NAME
PD NOTE CAPS, ROTATED ALONG THE STREET

NOTE

NOTE / ANNOTATION
PD NOTE

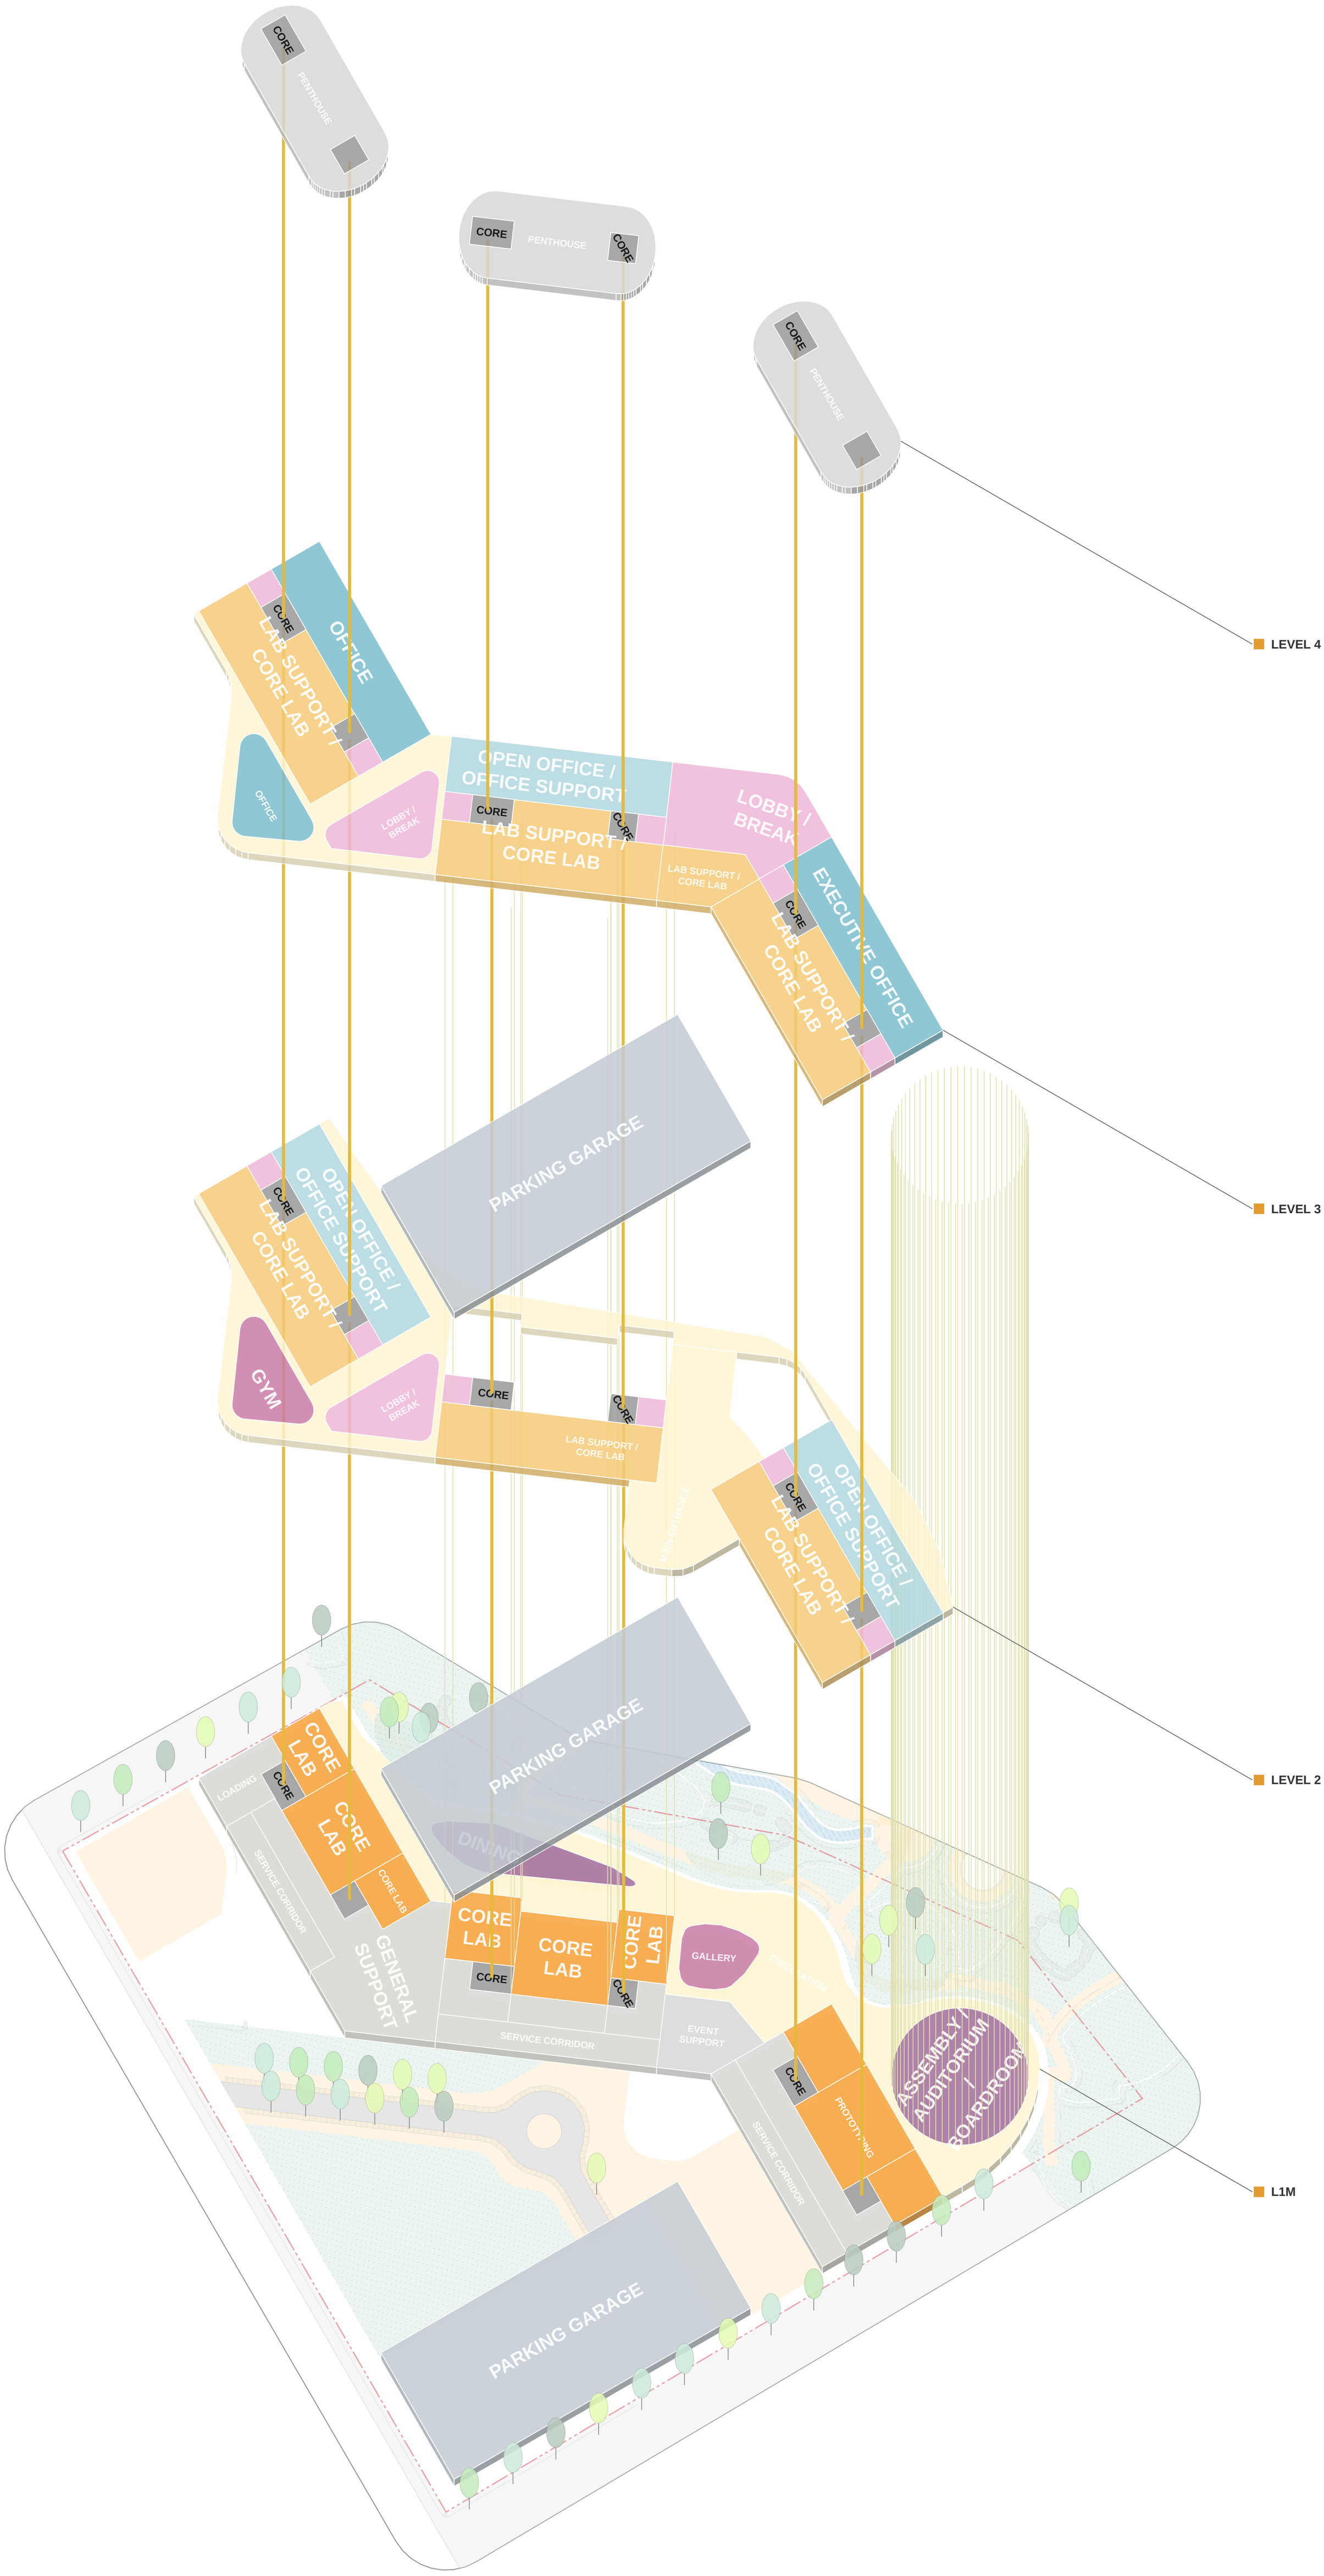

EXPLODED AXON B

N

SCALE 1/64" = 1'-0"

AXON LEGEND



TAG
ROUNDED LABEL + LEADER



PEDESTRIAN FLOW
#E47200 4 PT DASH



VEHICLE FLOW
#6C6C6C 4 PT DASH



TRANSIT STOP
#2F6DB5 ICON



VIEW / GATEWAY
#183C6C 2 PT DASH



SERVICE / LOADING
#6C6C6C ICON + TRIANGLE



ENTRY
#18427E ICON + TRIANGLE



VIEW MARKER
#D8AE78, WHITE NUMBER, LEADER

TREE
CANOPY CIRCLE (PLAN) / LOLLIPOP (AXON)

FUTURE BLDG

FUTURE BUILDING
CONTEXT LABEL: PD CONTEXT LABEL STYLE

MAIN ST

STREET NAME
PD NOTE CAPS, ROTATED ALONG THE STREET

NOTE


NOTE / ANNOTATION
PD NOTE



FLOOR KEY AXON L1M

SCALE 1/64" = 1'-0"


N

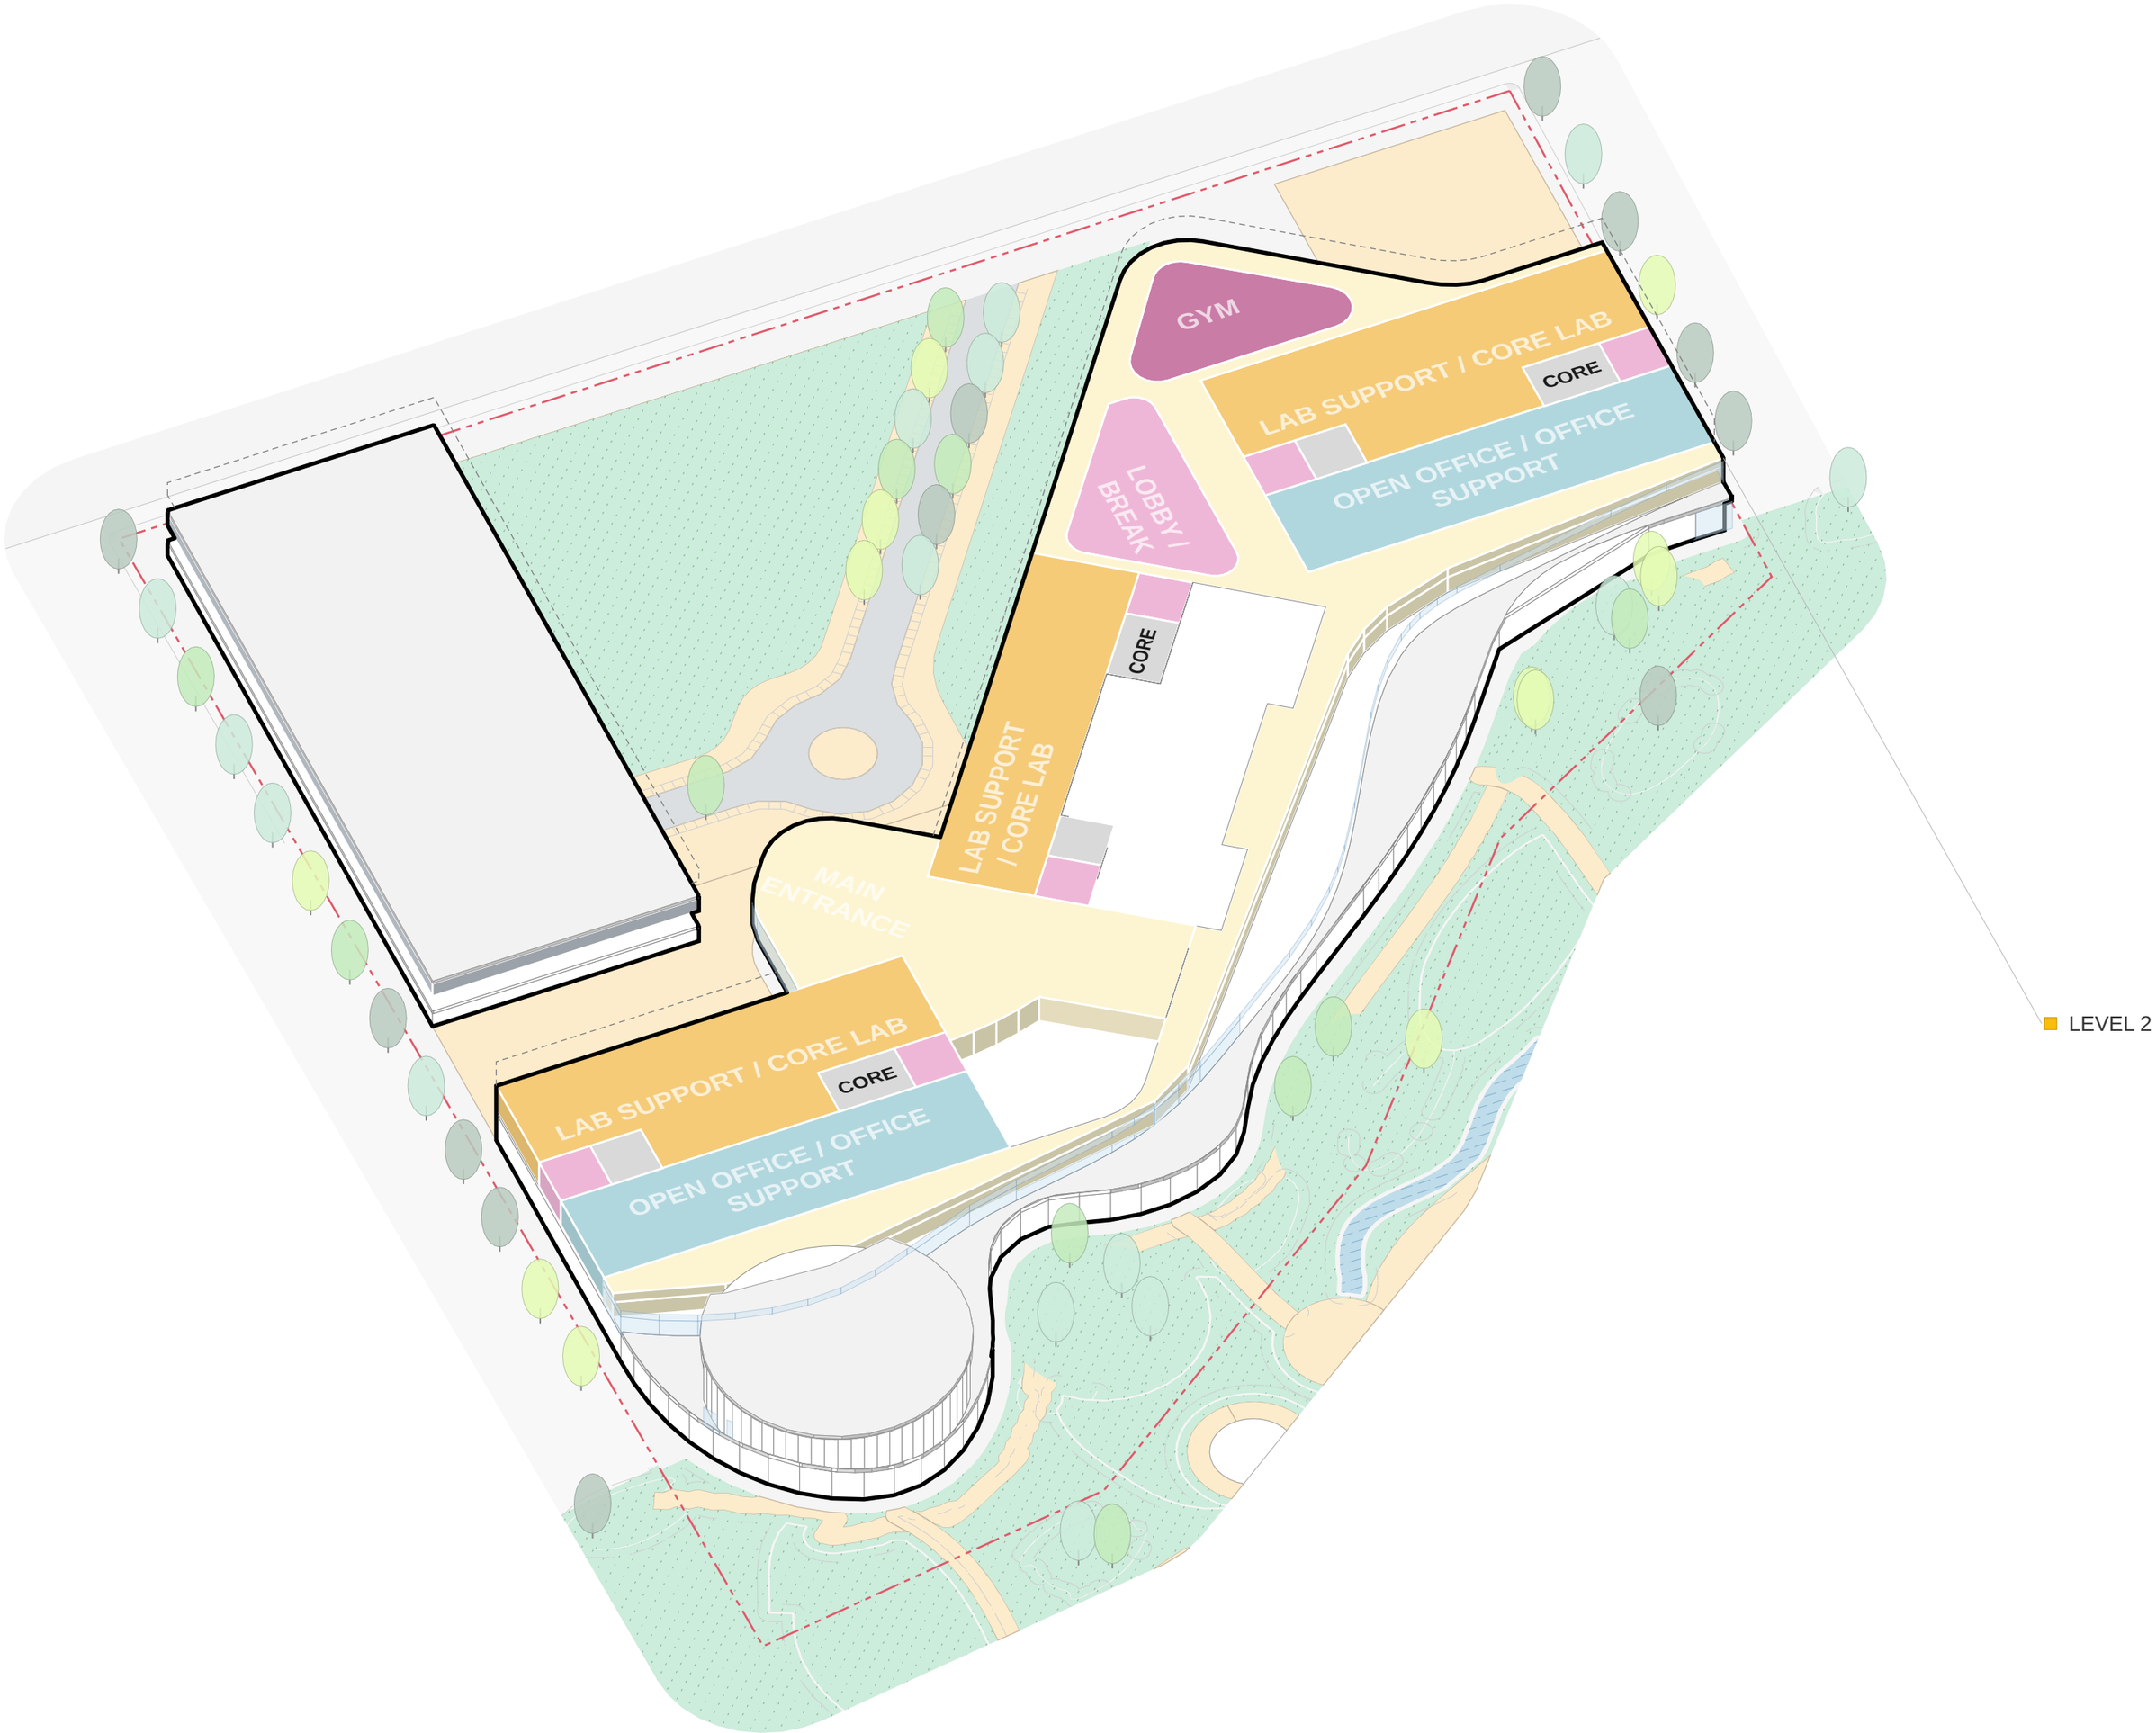

FLOOR KEY AXON LEVEL 2

SCALE 1/64" = 1'-0"

N

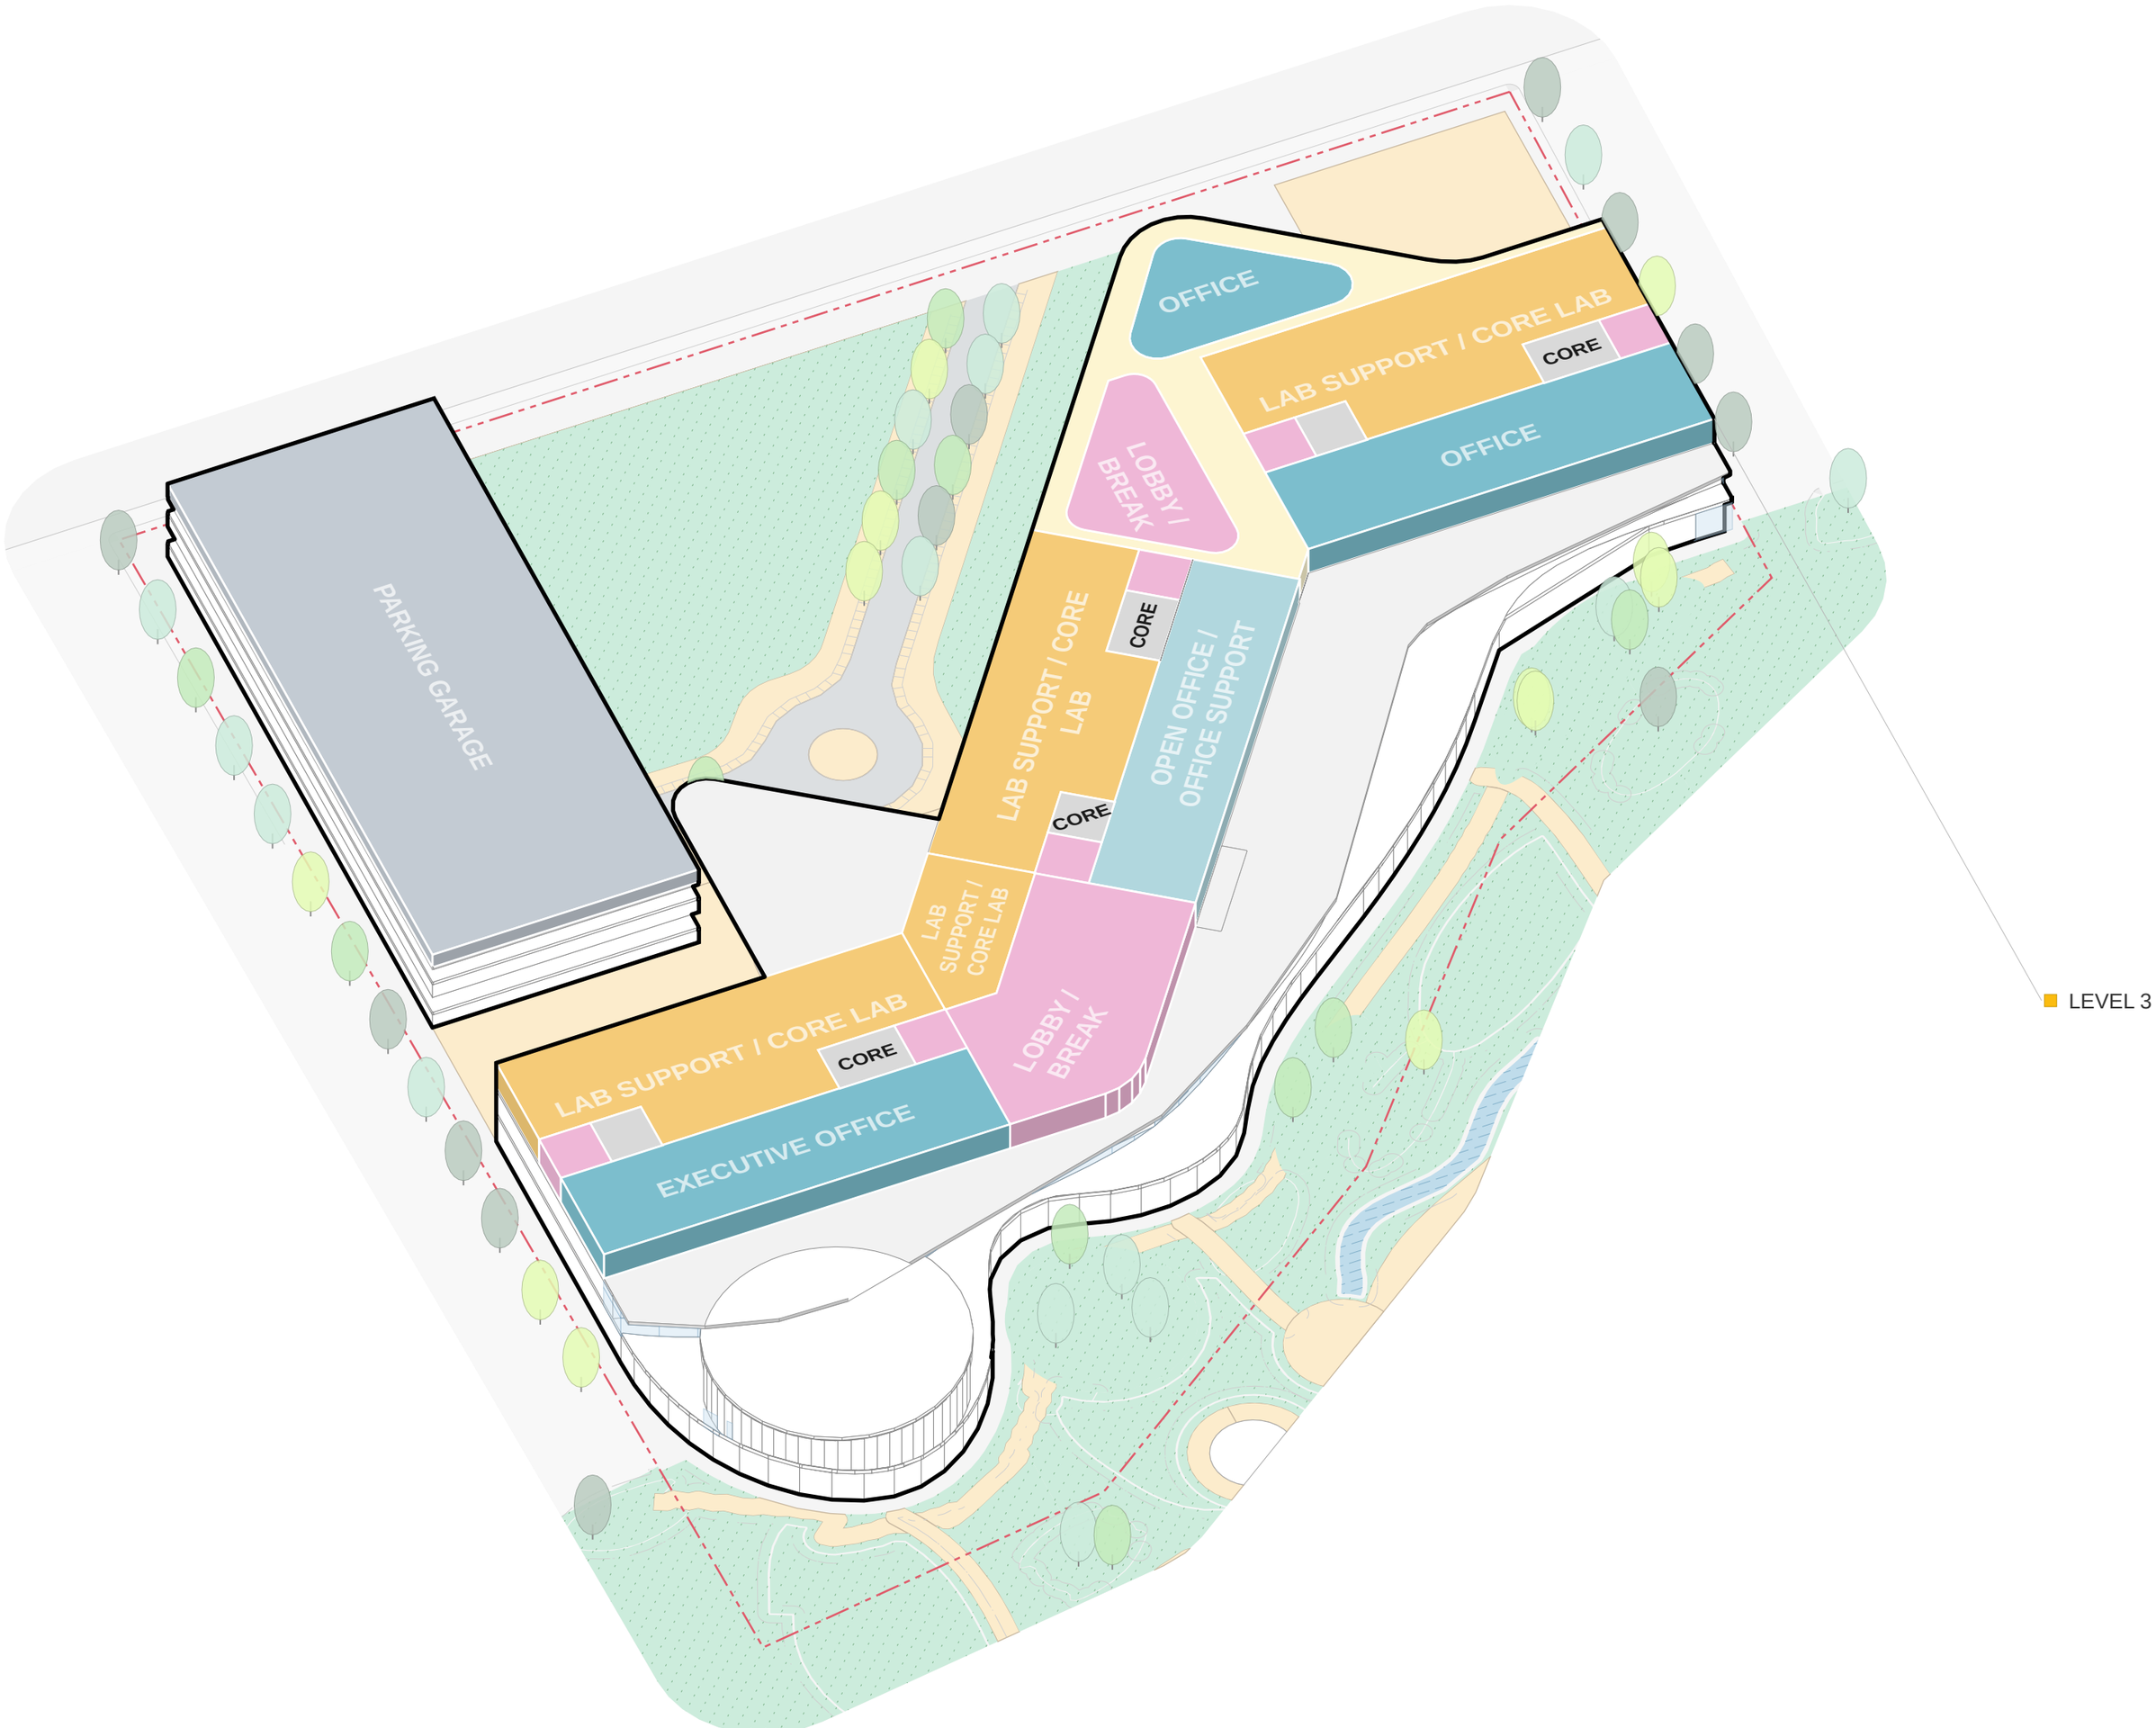

FLOOR KEY AXON LEVEL 3

SCALE 1/64" = 1'-0"

N



FLOOR KEY AXON LEVEL 4

SCALE 1/64" = 1'-0"

N

AXON LEGEND



TAG
ROUNDED LABEL + LEADER



PEDESTRIAN FLOW
#E47200 4 PT DASH



VEHICLE FLOW
#6C6C6C 4 PT DASH



TRANSIT STOP
#2F6DB5 ICON



VIEW / GATEWAY
#183C6C 2 PT DASH



SERVICE / LOADING
#6C6C6C ICON + TRIANGLE



ENTRY
#18427E ICON + TRIANGLE



VIEW MARKER
#D8AE78, WHITE NUMBER, LEADER

TREE
CANOPY CIRCLE (PLAN) / LOLLIPOP (AXON)

FUTURE BLDG

FUTURE BUILDING
CONTEXT LABEL: PD CONTEXT LABEL STYLE

MAIN ST

STREET NAME
PD NOTE CAPS, ROTATED ALONG THE STREET

NOTE

NOTE / ANNOTATION
PD NOTE

DETAILED PROGRAM PROPOSAL

BUILDING SUPPORT / MECHANICAL / STORAGE

L1M
SERVICE CORRIDOR

BUILDING SUPPORT / MECHANICAL / STORAGE

GENERAL SUPPORT

EVENT SUPPORT

LOADING

L4
PENTHOUSE

76,327 GSF

LAB

L1M
CORE LAB



PROTOTYPING



34,999 GSF

CORE

L1M
CORE



L2
CORE



L3
CORE



L4
CORE



17,417 GSF

PARKING

L1M
PARKING GARAGE



L2
PARKING GARAGE



L3
PARKING GARAGE


111,574 GSF

ASSEMBLY / AUDITORIUM / BOARDROOM

L1M
DINING



ASSEMBLY / AUDITORIUM / BOARDROOM

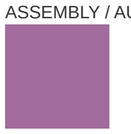


15,911 GSF

CONFERENCE

L1M
GALLERY



L2
GYM

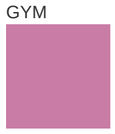

7,342 GSF

CIRCULATION

L1M
CIRCULATION

L2
CIRCULATION


MAIN ENTRANCE

L3
CIRCULATION


78,480 GSF

LOBBY / BREAK

L2
LOBBY / BREAK

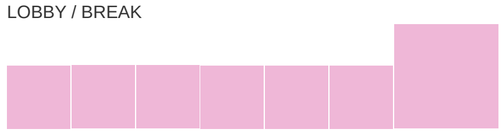


L3
LOBBY / BREAK

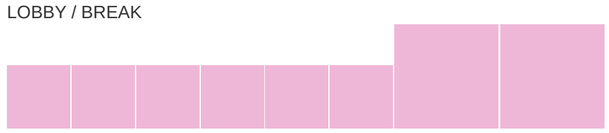


25,752 GSF

OPEN OFFICE / OFFICE SUPPORT

L2
OPEN OFFICE / OFFICE SUPPORT

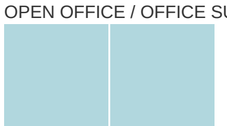

L3
OPEN OFFICE / OFFICE SUPPORT

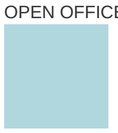


27,693 GSF

LAB SUPPORT / CORE LAB

L2
LAB SUPPORT / CORE LAB

L3
LAB SUPPORT / CORE LAB

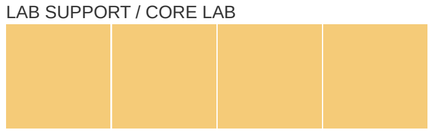

68,749 GSF

OFFICE

L3
OFFICE




EXECUTIVE OFFICE



22,703 GSF

MODEL (GSF) — TOTAL 486,946 GSF

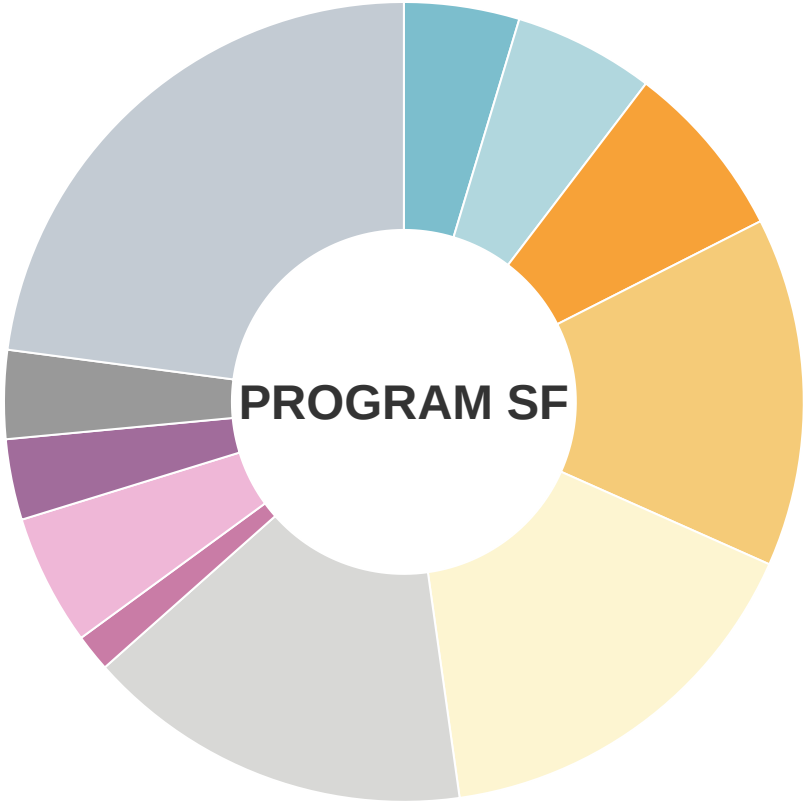


TOTAL: 486,946 GSF

- OFFICE 22,703 SF
- OPEN OFFICE / OFFICE SUPPORT 27,693 SF
- LAB 34,999 SF
- LAB SUPPORT / CORE LAB 68,749 SF
- CIRCULATION 78,480 SF
- BUILDING SUPPORT / MECHANICAL / STORAGE 76,327 SF
- CONFERENCE 7,342 SF
- LOBBY / BREAK 25,752 SF
- ASSEMBLY / AUDITORIUM / BOARDROOM 15,911 SF
- CORE 17,417 SF
- PARKING 111,574 SF

PROGRAM DEVELOPMENT SUMMARY

486,946 GSF



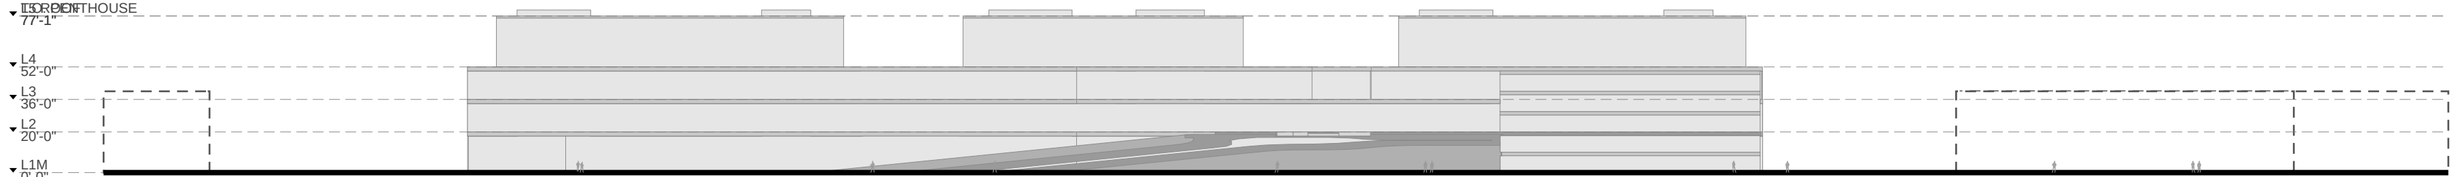

ELEVATION E1

SCALE 1/64" = 1'-0"



ELEVATION E2

SCALE 1/64" = 1'-0"