ANNOTATION SYMBOLS



ENTRY
#18427E ICON + TRIANGLE



SERVICE / LOADING
#6C6C6C ICON + TRIANGLE



VIEW MARKER
#D8AE78, WHITE NUMBER, LEADER



PARKING / CAR
#6C6C6C TOP VIEW



PEDESTRIAN FLOW
#E47200 4 PT DASH



VEHICLE FLOW
#6C6C6C 4 PT DASH



VIEW / GATEWAY
#183C6C 2 PT DASH



TRANSIT STOP
#2F6DB5 ICON

TREE
CANOPY CIRCLE (PLAN) / LOLLIPOP (AXON)



TAG
ROUNDED LABEL + LEADER

FUTURE BLDG

FUTURE BUILDING
CONTEXT LABEL: PD CONTEXT LABEL STYLE

MAIN ST

STREET NAME
PD NOTE CAPS, ROTATED ALONG THE STREET

NOTE

NOTE / ANNOTATION
PD NOTE

SCALE 1" = 100'-0"
0
400'
N

COMBINABLE CLASSROOMS
MEP SUPPORT
STORAGE
LOADING DOCK
CORE
CORE LABS
AUDITORIUM
CIRCULATION
FITNESS
QUANTUM HIGH MIP
COFFEE KIOSK
PROTOTYPING / FABRICATION
BUILDING SUPPORT / MECHANICAL / STORAGE
PARKING GARAGE

- LAB
- CONFERENCE
- CORE
- CIRCULATION
- LOBBY / BREAK
- PARKING
- BUILDING SUPPORT / MECHANICAL / STORAGE
- ASSEMBLY / AUDITORIUM / BOARDROOM

SITE PLAN

SCALE 1" = 100'-0"

0 400' N

OFFICE
BUILDING SUPPORT / MECHANICAL / STORAGE
ASSEMBLY / AUDITORIUM / BOARDROOM
PARKING
LAB
CONFERENCE
CORE
CIRCULATION
LOBBY / BREAK
SHELL / PENTHOUSE

SITE PLAN - ROOF

PROGRAM

- OFFICE
- OPEN OFFICE / OFFICE SUPPORT
- LAB
- LAB SUPPORT / CORE LAB
- CIRCULATION
- BUILDING SUPPORT / MECHANICAL / STORAGE
- VIVARIUM
- VIVARIUM SUPPORT
- VIVARIUM PROCEDURE
- CONFERENCE
- LOBBY / BREAK
- INTERACTION / COLLAB
- ASSEMBLY / AUDITORIUM / BOARDROOM
- CLINIC
- CLINIC SUPPORT
- GREEN ROOF / SKY GARDEN
- CORE
- STAIR / TRANSPORTATION
- SHELL / PENTHOUSE
- VOID
- UNASSIGNED
- PARKING

SITE / CONTEXT / NC

- NC.SCREEN
- NC.STRUCTURE
- NC.ROOF
- NC.GREEN
- NC.HARDSCAPE
- NC.TREE
- NC.WATER
- NC.INTERIOR
- NC.FURNITURE
- NC.MASSING
- NC.PROPERTYLINE
- BG.BUILDING
- BG.ROAD
- BG.HARDSCAPE
- BG.LANDSCAPE
- BG.TREE
- BG.WATER
- BG.LINE
- ENTOURAGE

LINES

- BUILDING OUTLINE
- ROOM DIVIDER
- GLASS LINE
- OPEN TO BELOW
- LEADER
- HARDSCAPE EDGE
- SITE / ROAD EDGE

ANNOTATION

N SCALE 1" = 100'-0"

0 200'

LEVEL 1

ANNOTATION SYMBOLS

ENTRY
#18427E ICON + TRIANGLE

SERVICE / LOADING
#6C6C6C ICON + TRIANGLE

1
VIEW MARKER
#D8AE78, WHITE NUMBER, LEADER

PARKING / CAR
#6C6C6C TOP VIEW

PEDESTRIAN FLOW
#E47200 4 PT DASH

VEHICLE FLOW
#6C6C6C 4 PT DASH

VIEW / GATEWAY
#183C6C 2 PT DASH

TRANSIT STOP
#2F6DB5 ICON

TREE
CANOPY CIRCLE (PLAN) / LOLLIPOP (AXON)

TAG
TAG
ROUNDED LABEL + LEADER

FUTURE BLDG
FUTURE BUILDING
CONTEXT LABEL: PD CONTEXT LABEL STYLE

MAIN ST
STREET NAME
PD NOTE CAPS, ROTATED ALONG THE STREET

NOTE
NOTE / ANNOTATION
PD NOTE

ENTOURAGE






L1
COMMUNITY CLASSROOMS
MEP SUPPORT
STORAGE
CORE LABS
LOCKER
LOCKER
AUDITORIUM
CIRCULATION
FITNESS
QUANTUM HIGH MIP
TOILET FACILITIES
MULTI-PURPOSE CLASSROOMS
BUILDING SUPPORT / MECHANICAL STORAGE
PARKING GARAGE
L2
PARTNERS / INCUBATORS
CONFERENCE
DINING HALL
CIRCULATION
OPEN TO BELOW
OFFICE
LOBBY
BREAK
RESEARCH
PARKING GARAGE
L3
RESEARCH
SEMINAR
OFFICE
LOBBY
BREAK
CIRCULATION
OPEN TO BELOW
PARKING GARAGE
L4
RESEARCH
OFFICE
SEMINAR
OPEN TO BELOW
LOBBY
BREAK
L5
SHELL / PENTHOUSE
OPEN TO BELOW
OFFICE
LOBBY
BREAK
RESEARCH
L6
SHELL / PENTHOUSE

SCALE 1" = 100'-0"
0
400'
N

COMBINABLE CLASSROOMS
MEP SUPPORT
CORE
STORAGE
LOADING DOCK
CORE LABS
AUDITORIUM
CIRCULATION
FITNESS
QUANTUM HIGH MIP
COFFEE KIOSK
PROTOTYPING / FABRICATION
BUILDING SUPPORT / MECHANICAL / STORAGE
PARKING GARAGE

- LAB
- CONFERENCE
- CORE
- CIRCULATION
- LOBBY / BREAK
- PARKING
- BUILDING SUPPORT / MECHANICAL / STORAGE
- ASSEMBLY / AUDITORIUM / BOARDROOM

LEVEL 1

SCALE 1" = 100'-0"

0 400'

N

PARTNER / INCUBATOR

CONFERENCE

DINING

PREP

CIRCULATION

OFFICE

OPEN TO BELOW

CORE

LOBBY / BREAK

RESEARCH

PARKING GARAGE

OFFICE
LAB
CIRCULATION
CONFERENCE
LOBBY / BREAK
CORE
PARKING

LEVEL 2

SCALE 1" = 100'-0"

0 400'

N

RESEARCH

SEMINAR

CORE

OFFICE

LOBBY / BREAK

CIRCULATION

CONFERENCE

OPEN TO BELOW

PARKING GARAGE


OFFICE
CONFERENCE
PARKING
LAB
LOBBY / BREAK
CIRCULATION
CORE

LEVEL 3

SCALE 1" = 100'-0"

0 400'

N

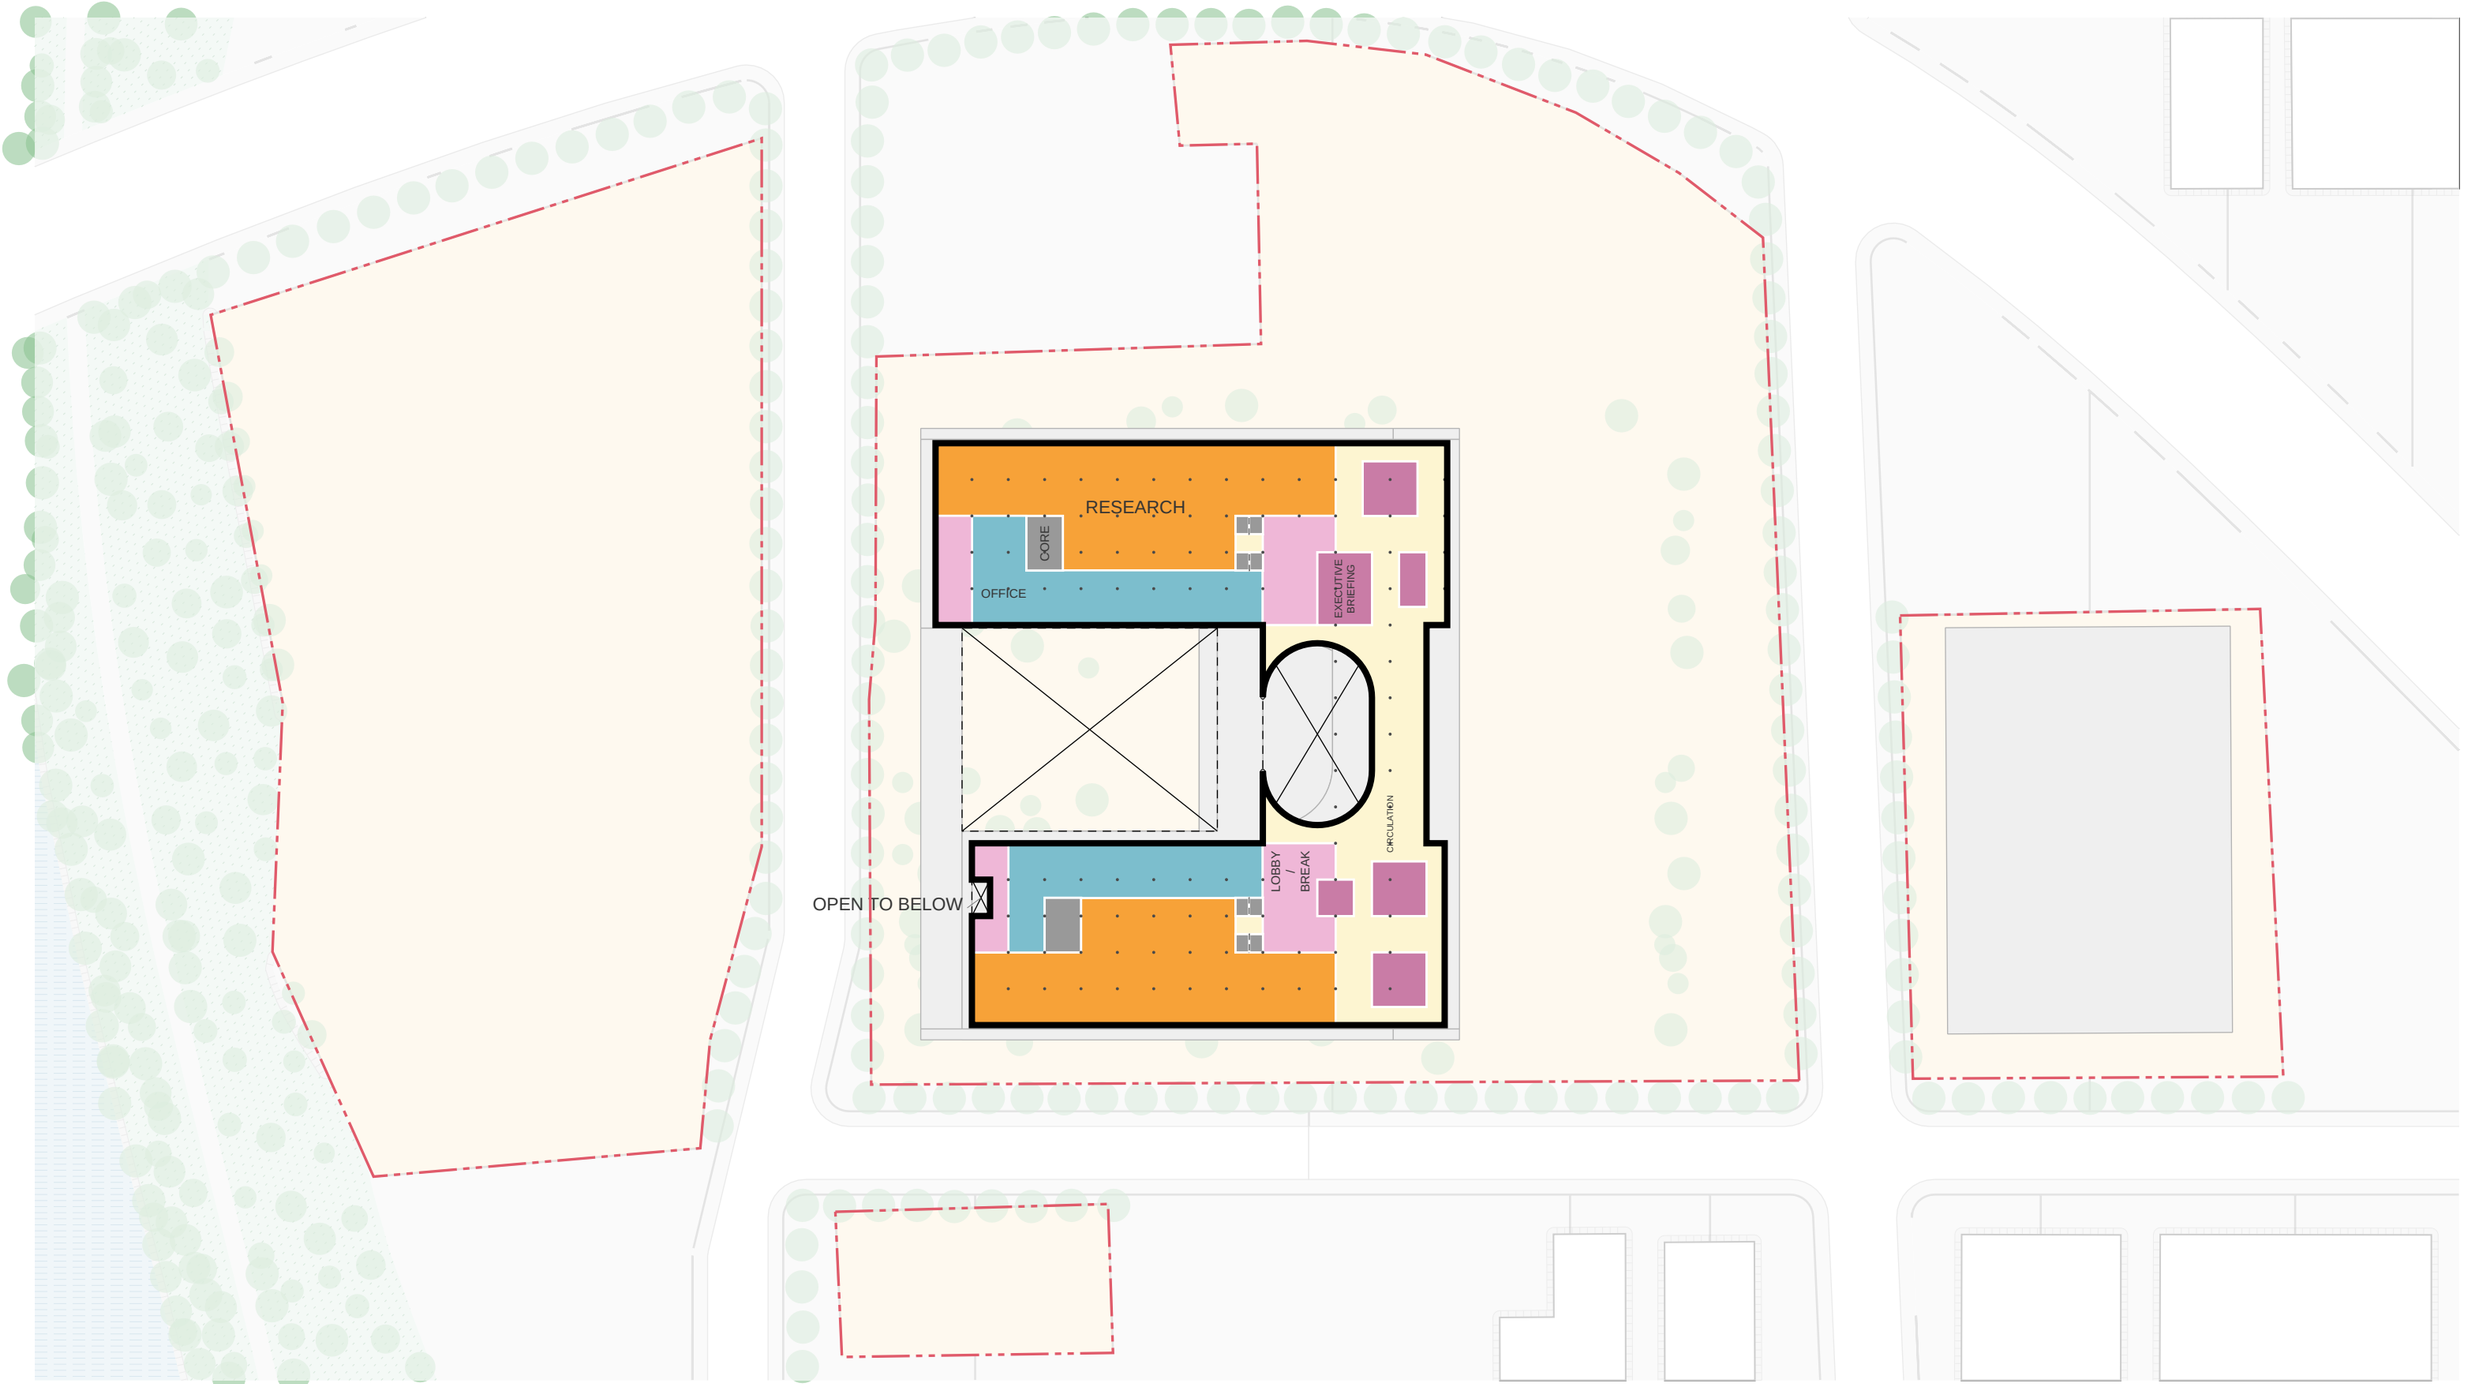

OFFICE
CONFERENCE
LAB
LOBBY / BREAK
CIRCULATION
CORE

LEVEL 4

SCALE 1" = 100'-0"
0
400'
N

CORE
SHELL / PENTHOUSE
OPEN TO BELOW
OFFICE
RESEARCH
LOBBY / BREAK

OFFICE
CORE
LAB
SHELL / PENTHOUSE
LOBBY / BREAK

LEVEL 5

SCALE 1" = 100'-0"

0 400'


N

CORE

SHELL / PENTHOUSE


■ CORE ▢ SHELL / PENTHOUSE

LEVEL 6

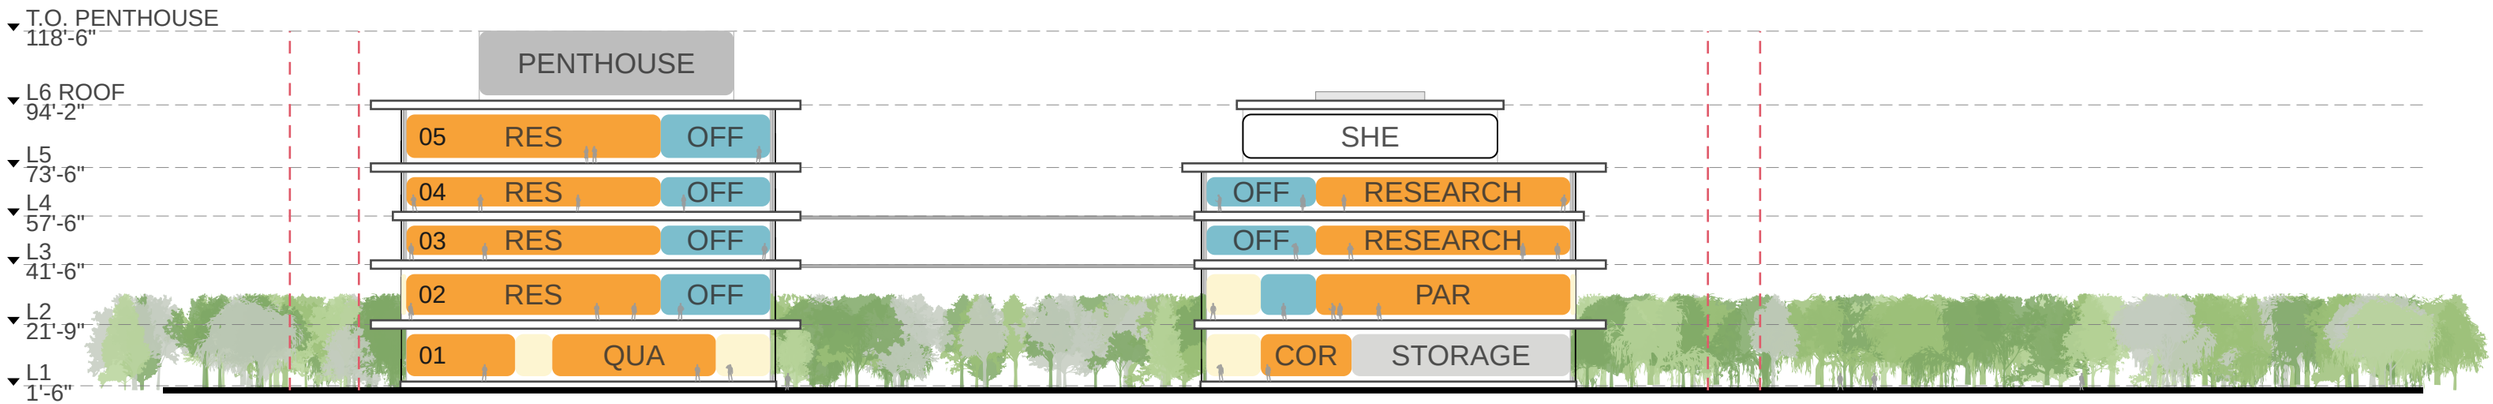


SECTION A

SCALE 1" = 50'-0"

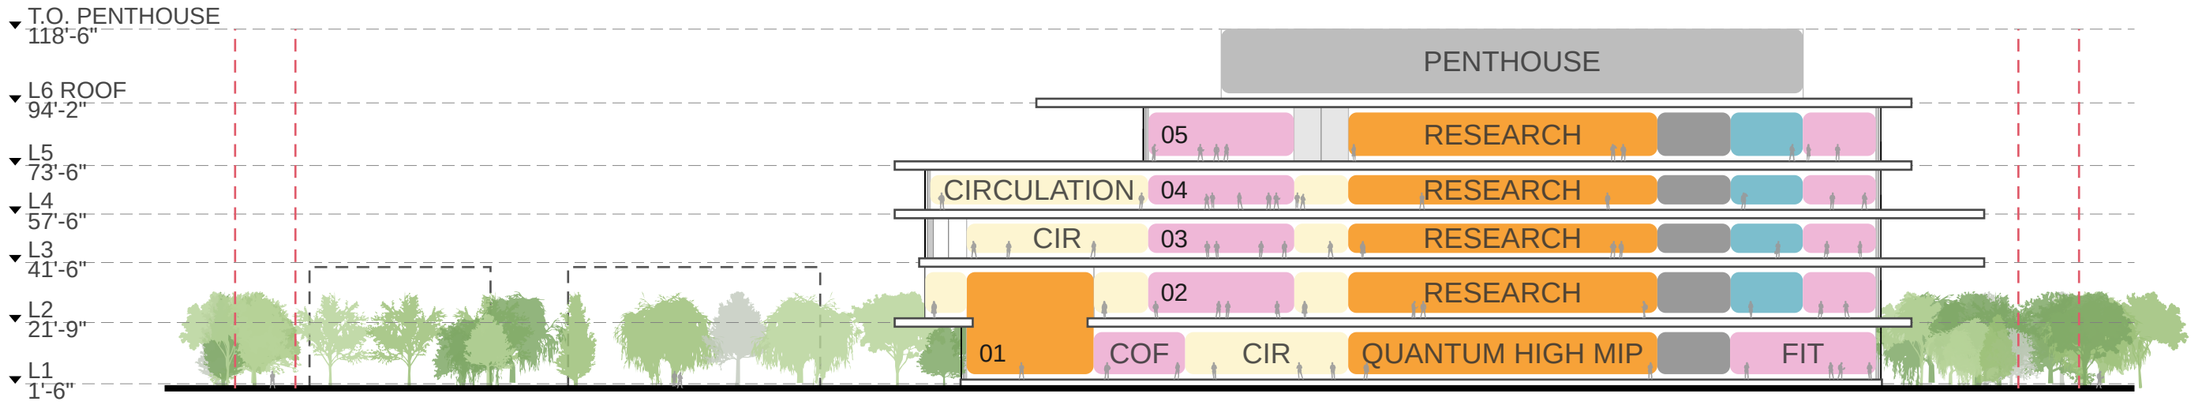


SECTION B

SCALE 1" = 50'-0"

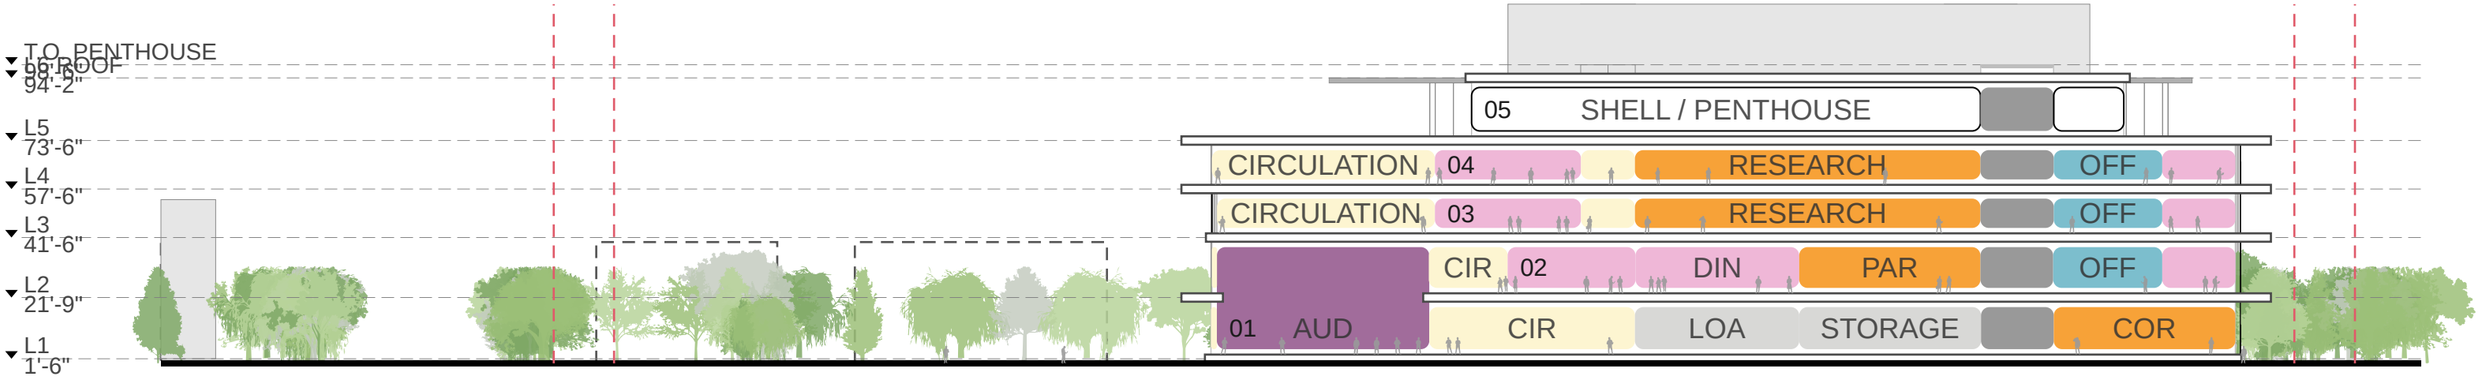

SECTION C

SCALE 1" = 50'-0"

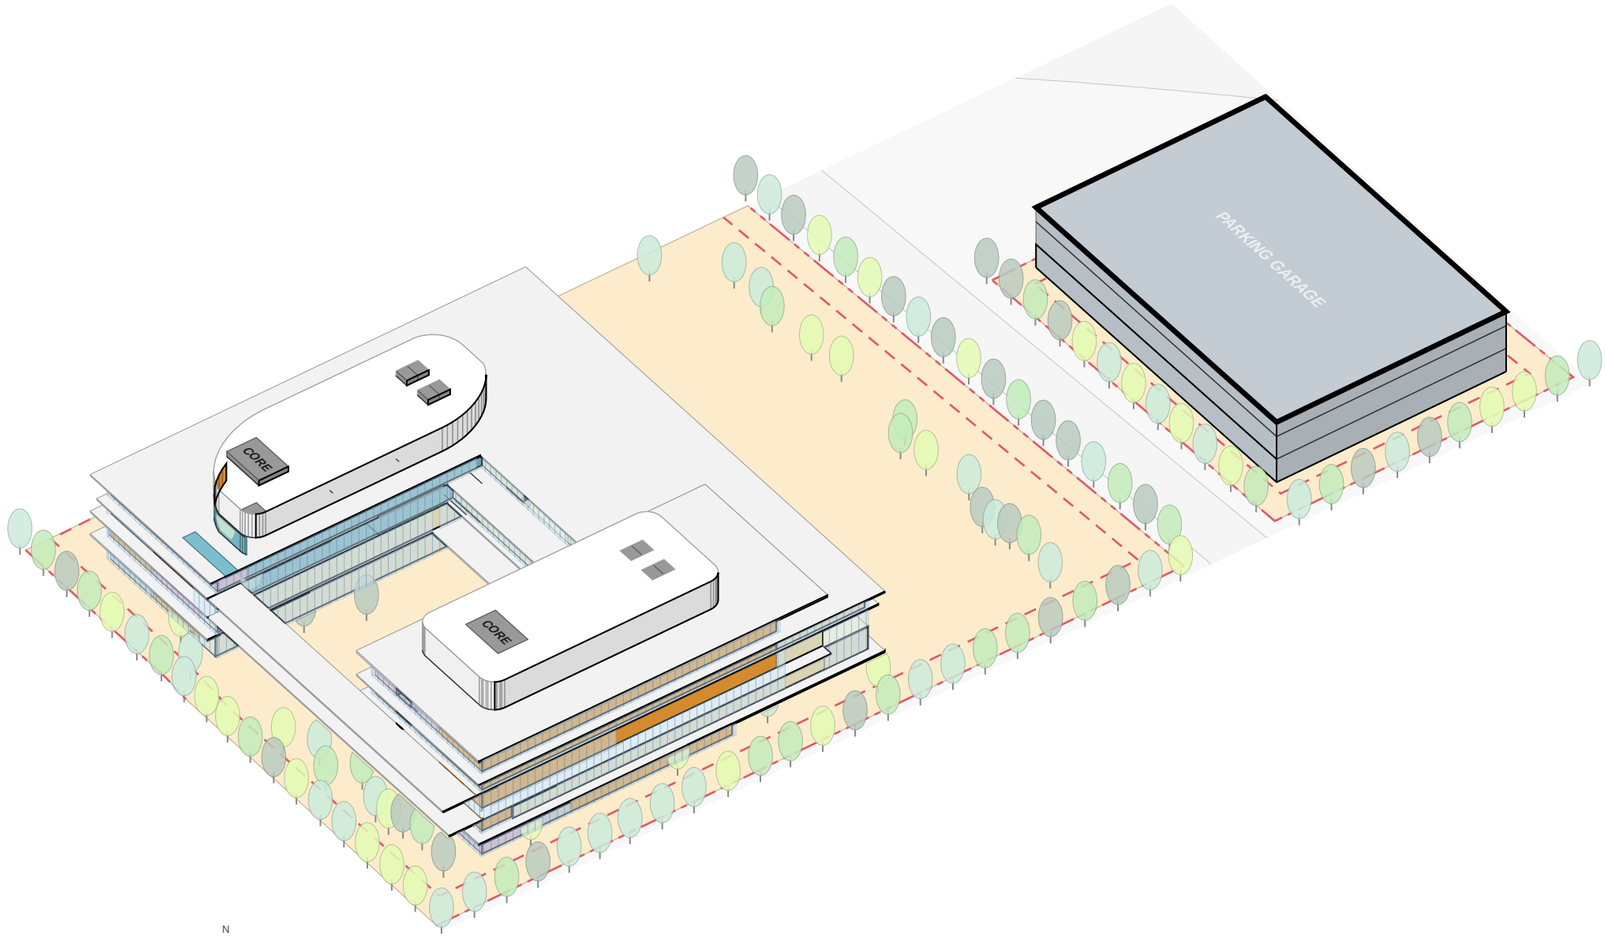

N

STACKED AXON

SCALE 1" = 100'-0"

AXON LEGEND



TAG
ROUNDED LABEL + LEADER



PEDESTRIAN FLOW
#E47200 4 PT DASH



VEHICLE FLOW
#6C6C6C 4 PT DASH



TRANSIT STOP
#2F6DB5 ICON



VIEW / GATEWAY
#183C6C 2 PT DASH



SERVICE / LOADING
#6C6C6C ICON + TRIANGLE



ENTRY
#18427E ICON + TRIANGLE



VIEW MARKER
#D8AE78, WHITE NUMBER, LEADER

TREE
CANOPY CIRCLE (PLAN) / LOLLIPOP (AXON)

FUTURE BLDG

FUTURE BUILDING
CONTEXT LABEL: PD CONTEXT LABEL STYLE

MAIN ST

STREET NAME
PD NOTE CAPS, ROTATED ALONG THE STREET

NOTE

NOTE / ANNOTATION
PD NOTE

AXON LEGEND



TAG
ROUNDED LABEL + LEADER



PEDESTRIAN FLOW
#E47200 4 PT DASH



VEHICLE FLOW
#6C6C6C 4 PT DASH



TRANSIT STOP
#2F6DB5 ICON



VIEW / GATEWAY
#183C6C 2 PT DASH



SERVICE / LOADING
#6C6C6C ICON + TRIANGLE



ENTRY
#18427E ICON + TRIANGLE



VIEW MARKER
#D8AE78, WHITE NUMBER, LEADER

TREE
CANOPY CIRCLE (PLAN) / LOLLIPOP (AXON)

FUTURE BLDG


FUTURE BUILDING
CONTEXT LABEL: PD CONTEXT LABEL STYLE

MAIN ST

STREET NAME
PD NOTE CAPS, ROTATED ALONG THE STREET


NOTE

NOTE / ANNOTATION
PD NOTE

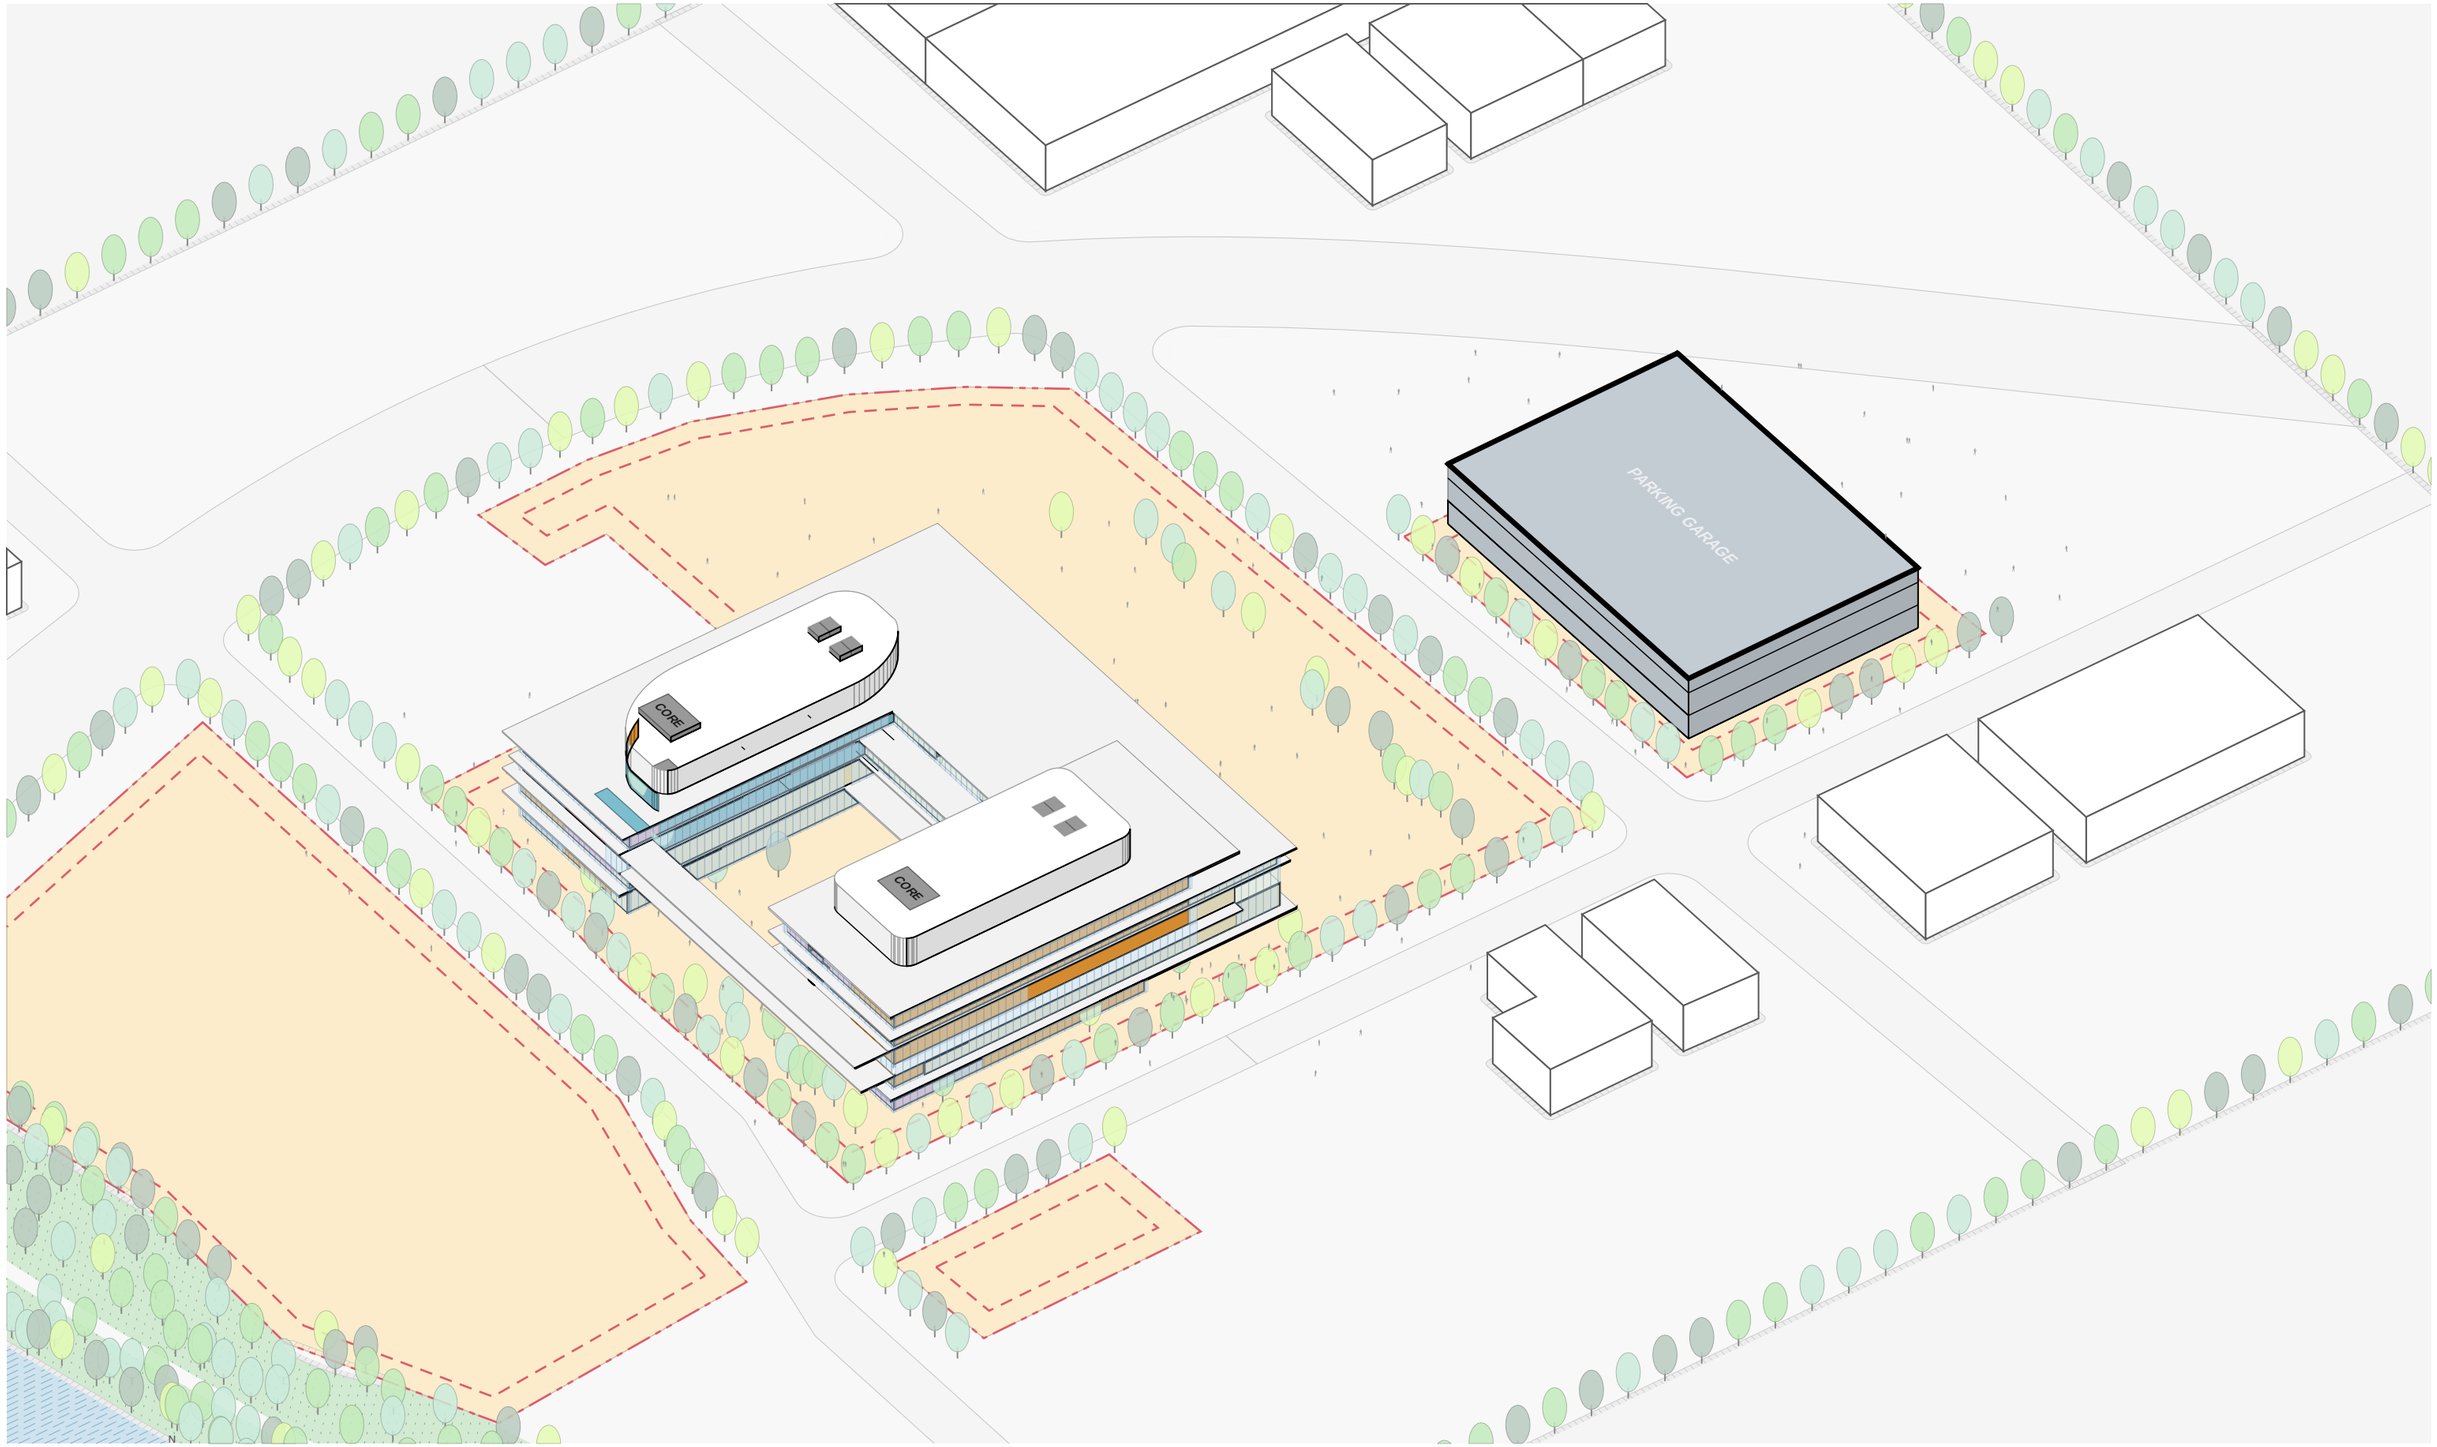

SITE AXON


SCALE 1" = 100'-0"

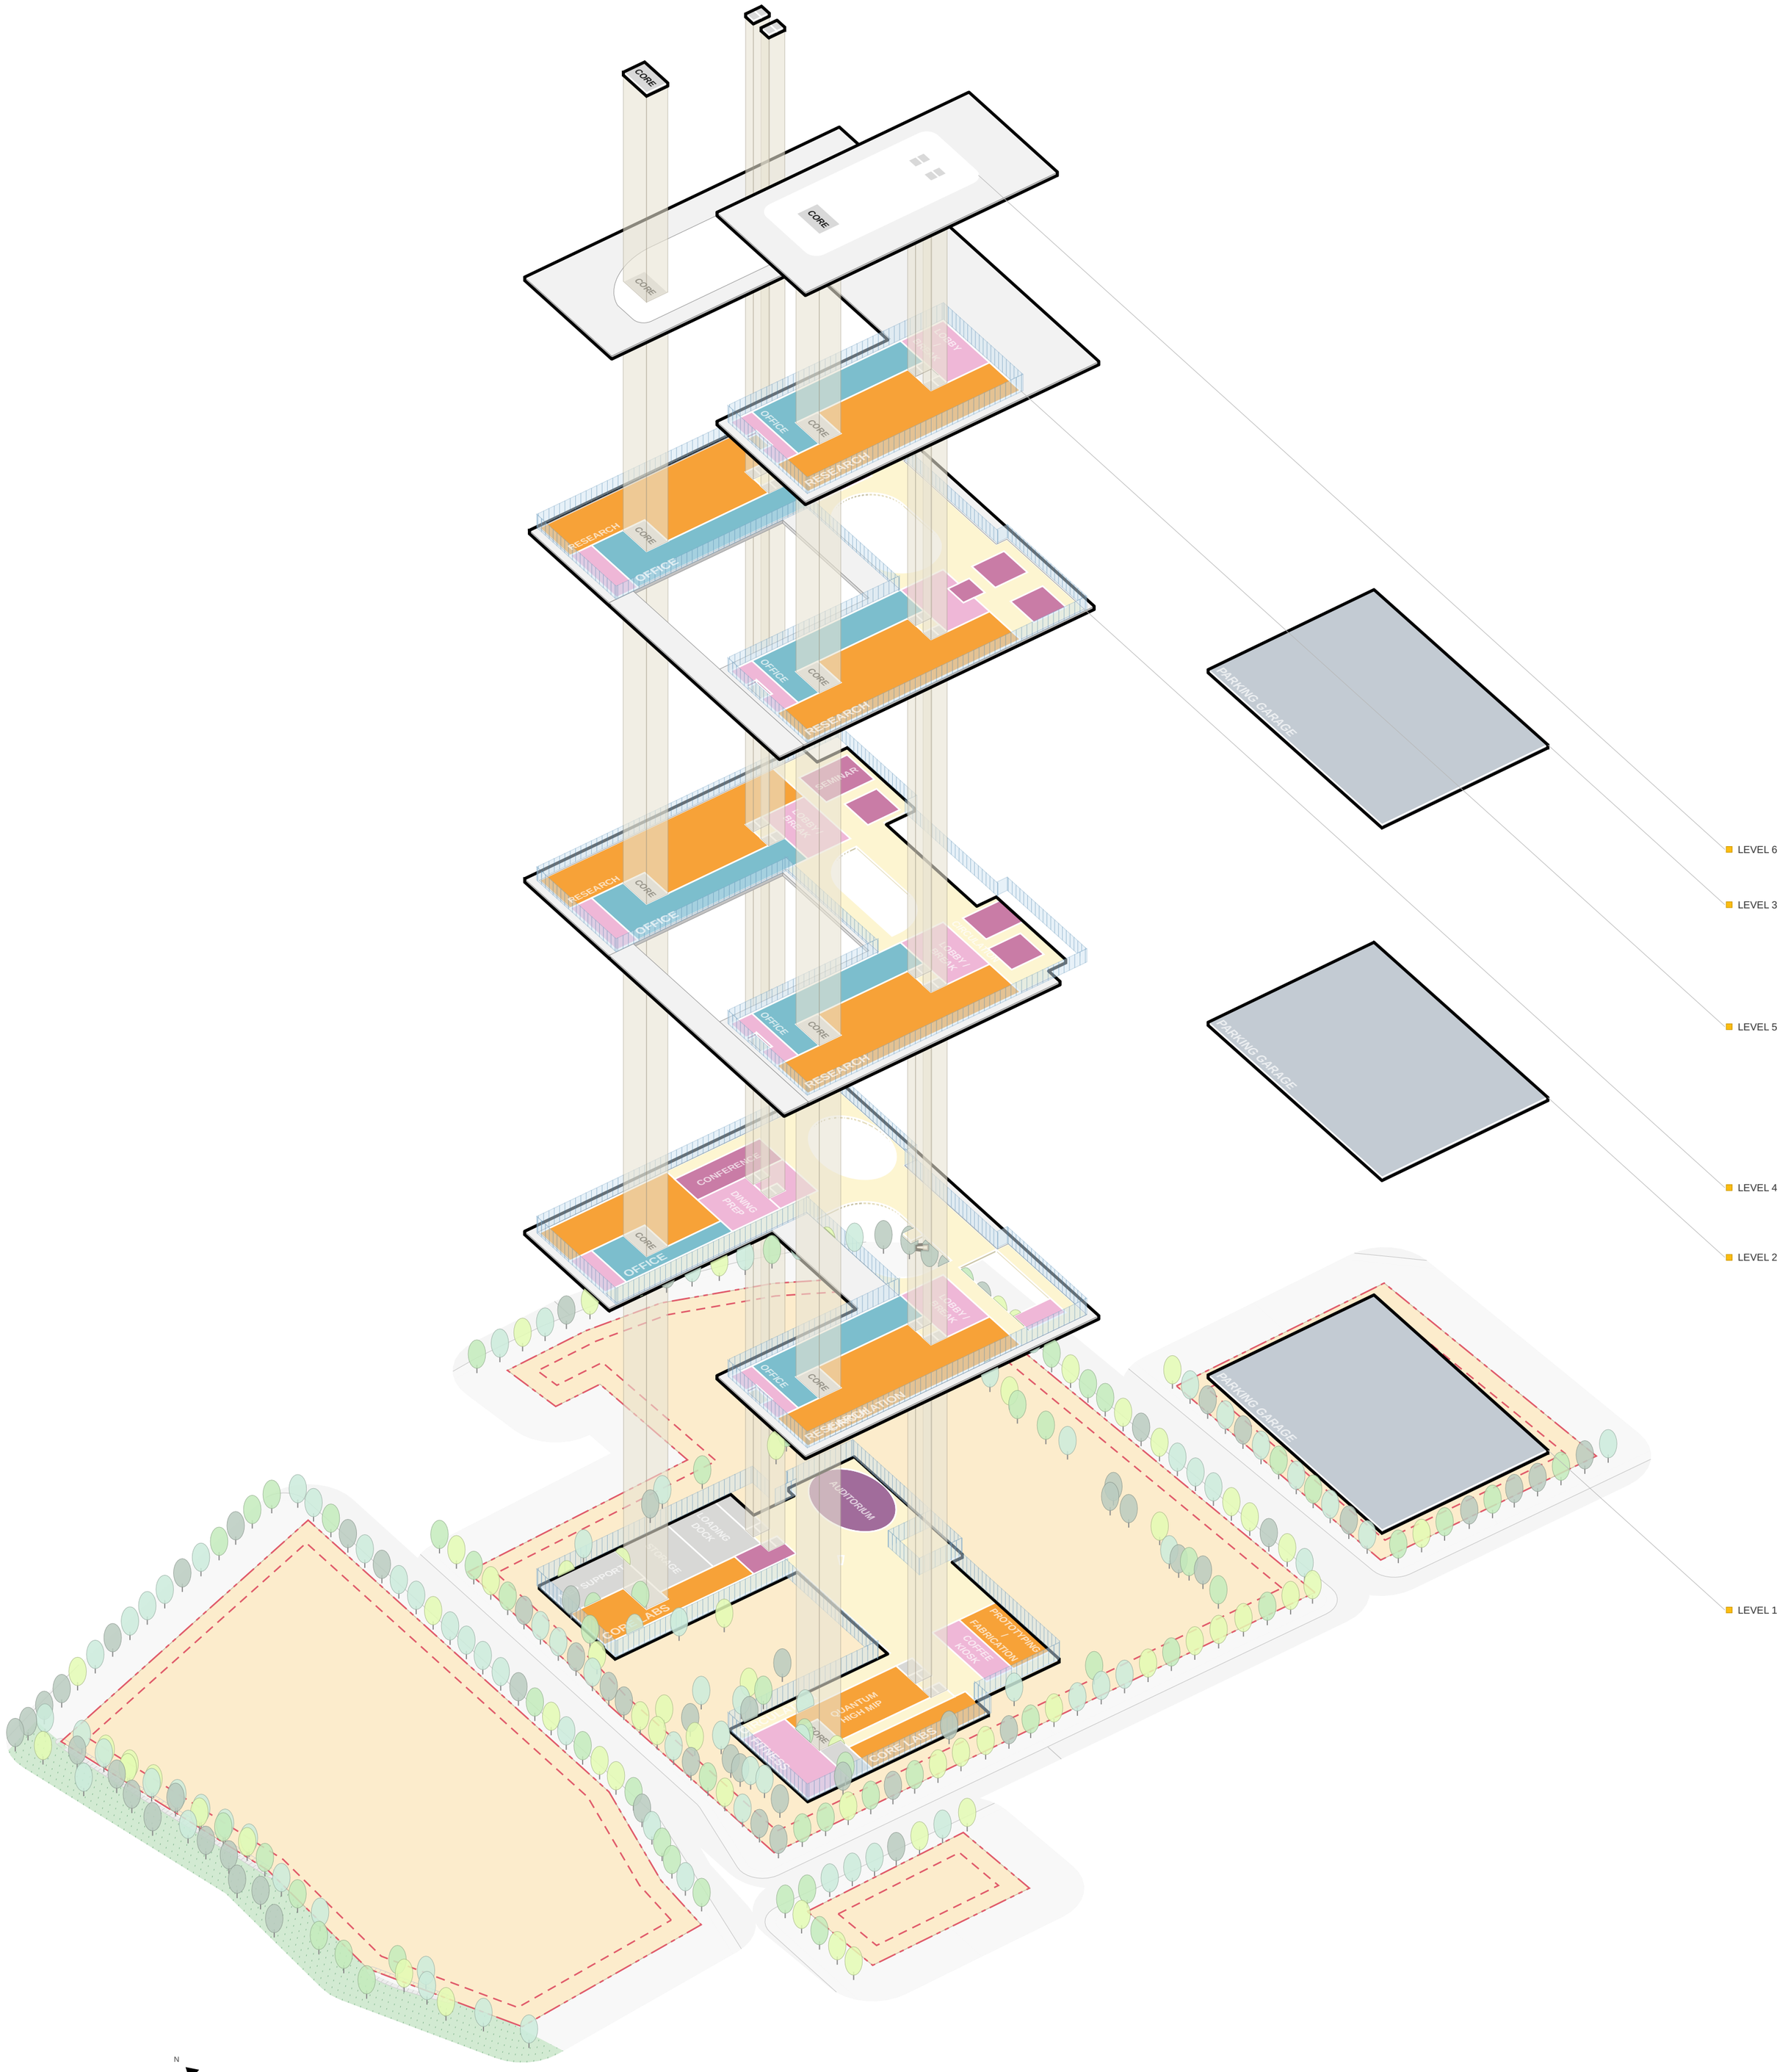

EXPLODED AXON

SCALE 1" = 100'-0"

N

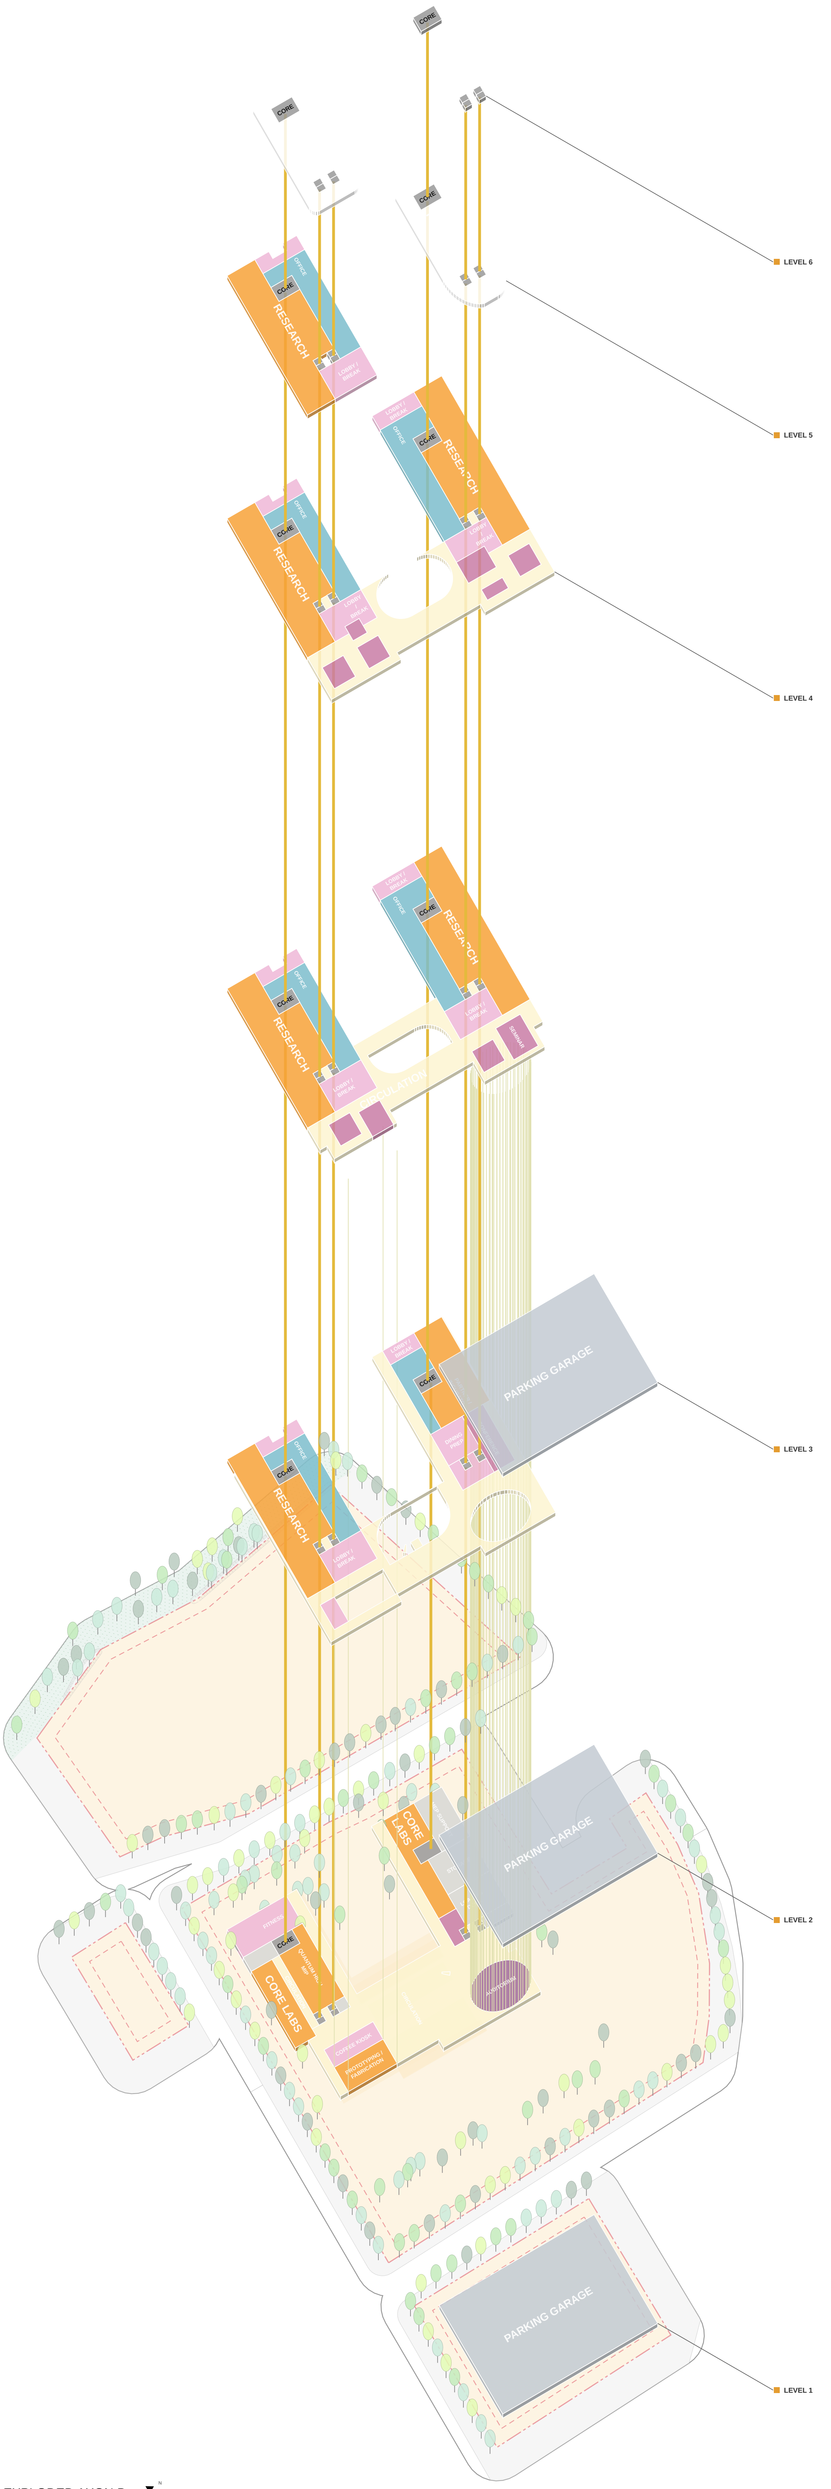

EXPLODED AXON B

SCALE 1" = 100'-0"

AXON LEGEND



TAG
ROUNDED LABEL + LEADER



PEDESTRIAN FLOW
#E47200 4 PT DASH



VEHICLE FLOW
#6C6C6C 4 PT DASH



TRANSIT STOP
#2F6DB5 ICON



VIEW / GATEWAY
#183C6C 2 PT DASH



SERVICE / LOADING
#6C6C6C ICON + TRIANGLE



ENTRY
#18427E ICON + TRIANGLE



VIEW MARKER
#D8AE78, WHITE NUMBER, LEADER

TREE
CANOPY CIRCLE (PLAN) / LOLLIPOP (AXON)

FUTURE BLDG

FUTURE BUILDING
CONTEXT LABEL: PD CONTEXT LABEL STYLE

MAIN ST

STREET NAME
PD NOTE CAPS, ROTATED ALONG THE STREET

NOTE

NOTE / ANNOTATION
PD NOTE

AXON LEGEND



TAG
ROUNDED LABEL + LEADER



PEDESTRIAN FLOW
#E47200 4 PT DASH



VEHICLE FLOW
#6C6C6C 4 PT DASH



TRANSIT STOP
#2F6DB5 ICON



VIEW / GATEWAY
#183C6C 2 PT DASH



SERVICE / LOADING
#6C6C6C ICON + TRIANGLE



ENTRY
#18427E ICON + TRIANGLE



VIEW MARKER
#D8AE78, WHITE NUMBER, LEADER

TREE
CANOPY CIRCLE (PLAN) / LOLLIPOP (AXON)

FUTURE BLDG


FUTURE BUILDING
CONTEXT LABEL: PD CONTEXT LABEL STYLE

MAIN ST

STREET NAME
PD NOTE CAPS, ROTATED ALONG THE STREET

NOTE


NOTE / ANNOTATION
PD NOTE

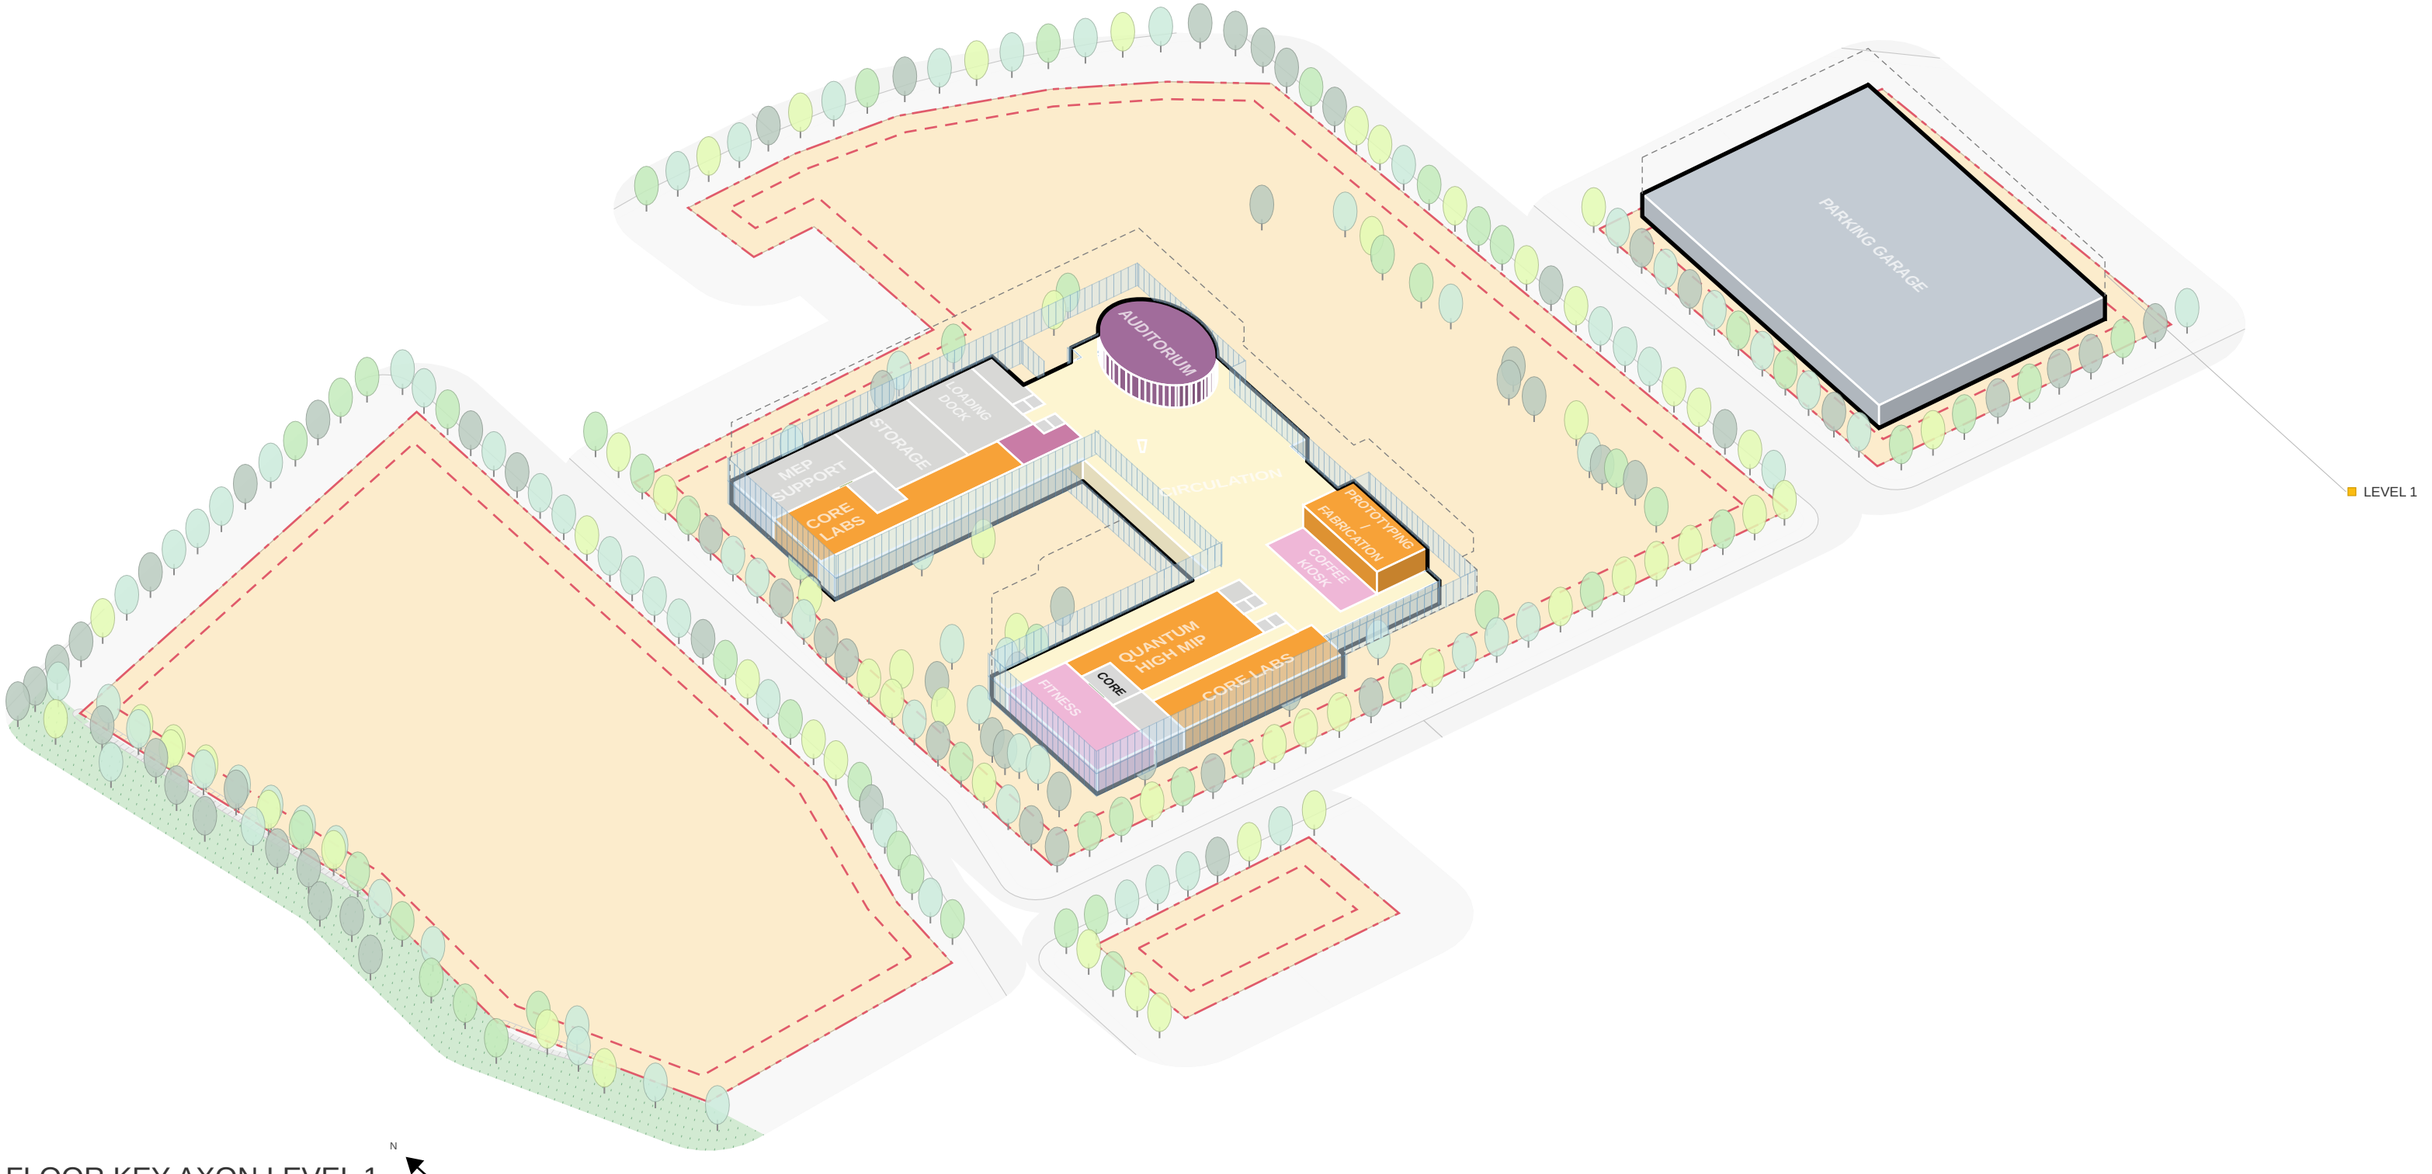

FLOOR KEY AXON LEVEL 1


SCALE 1" = 100'-0"

N

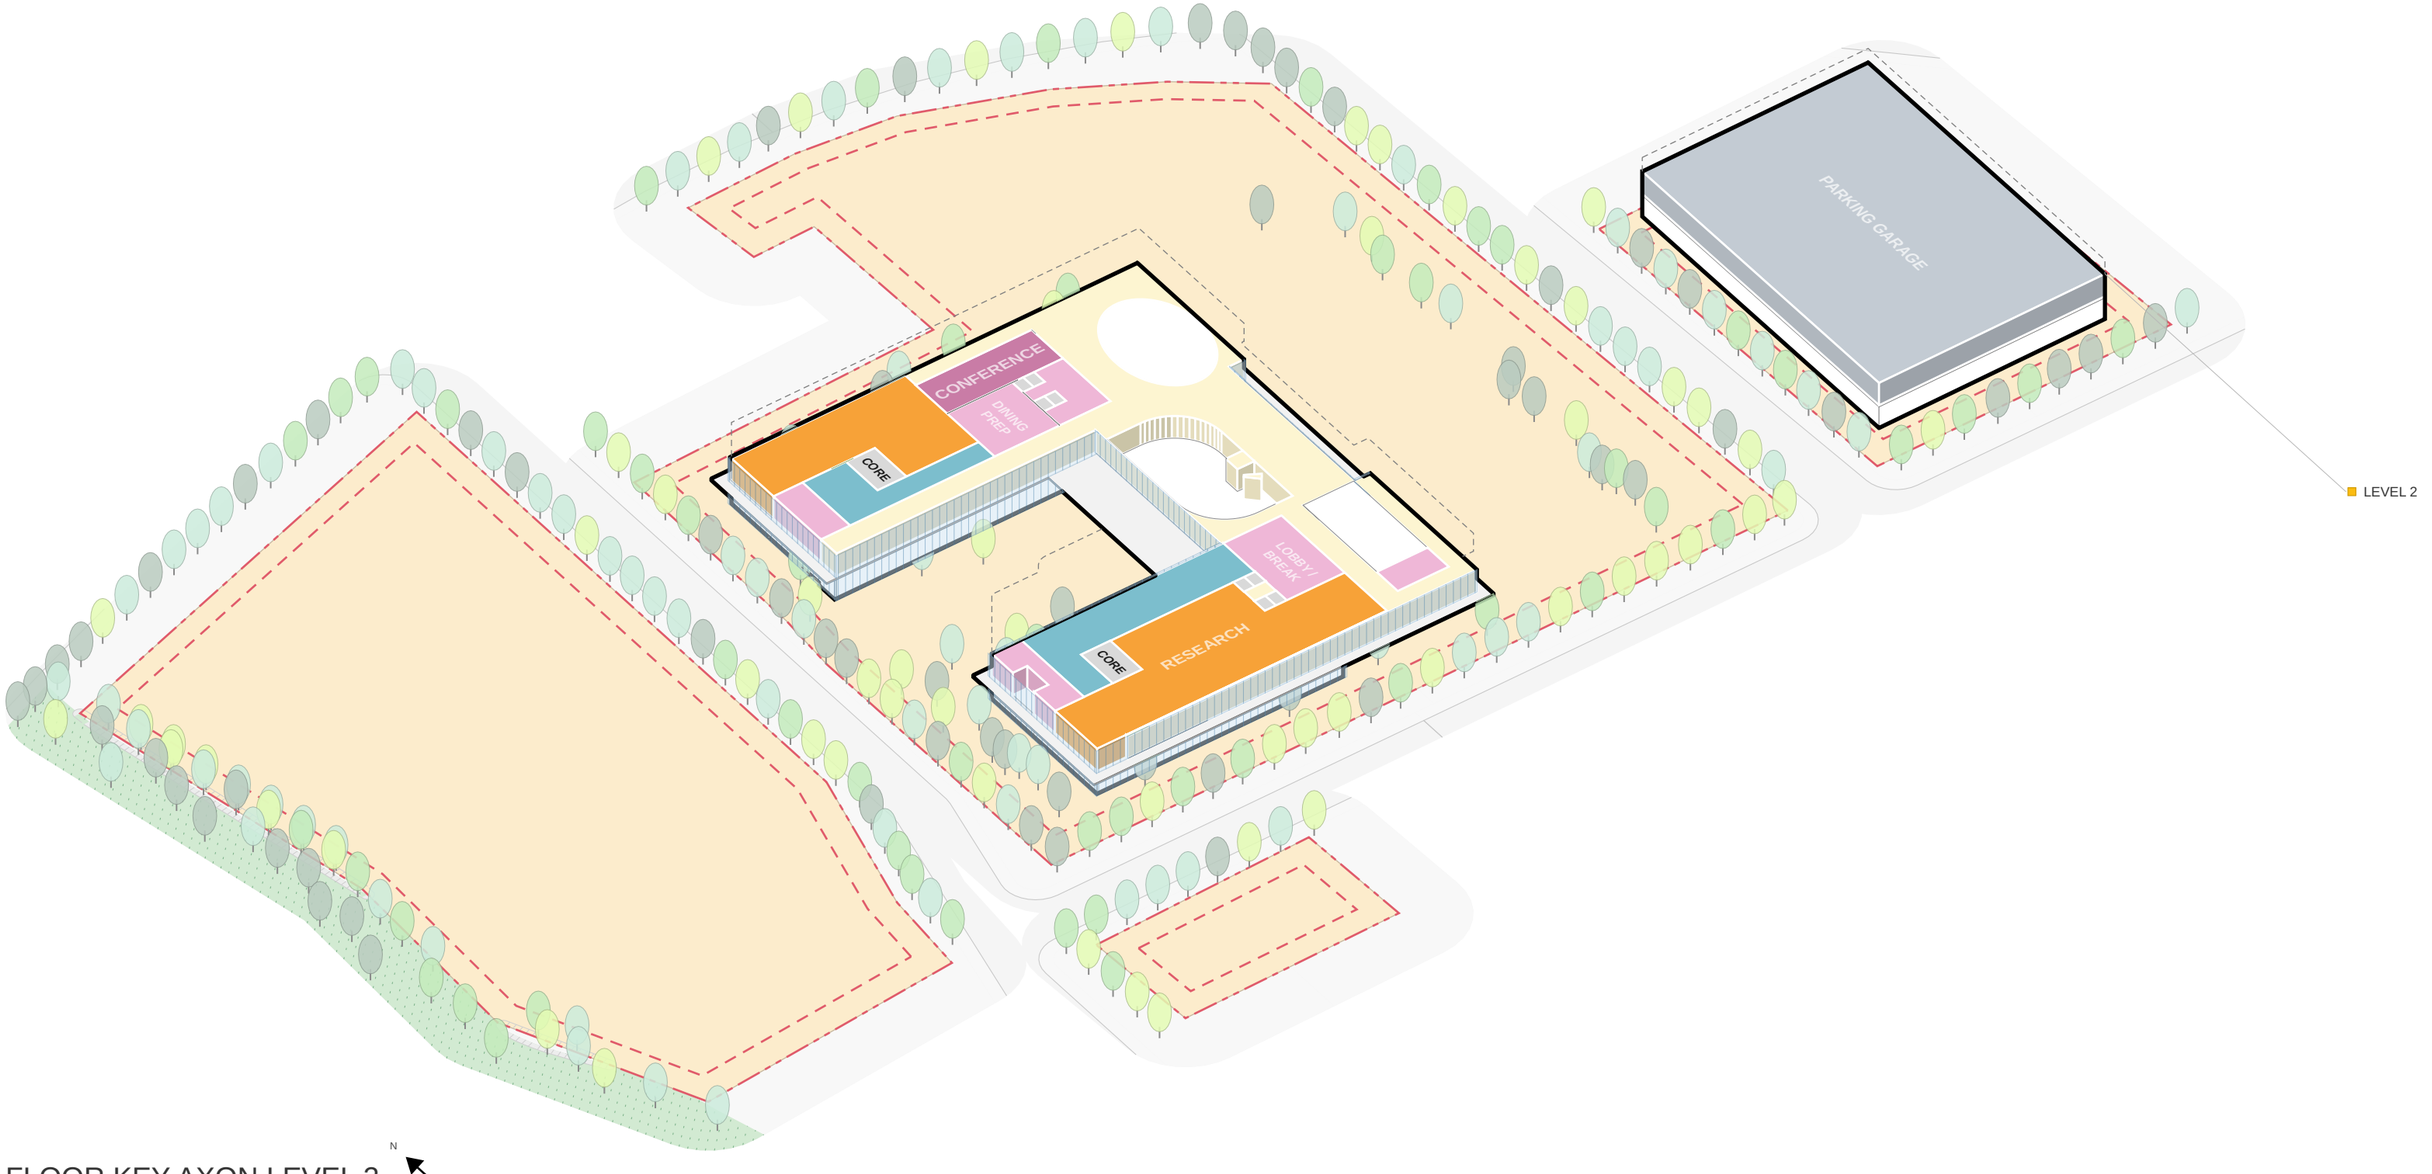

FLOOR KEY AXON LEVEL 2


SCALE 1" = 100'-0"

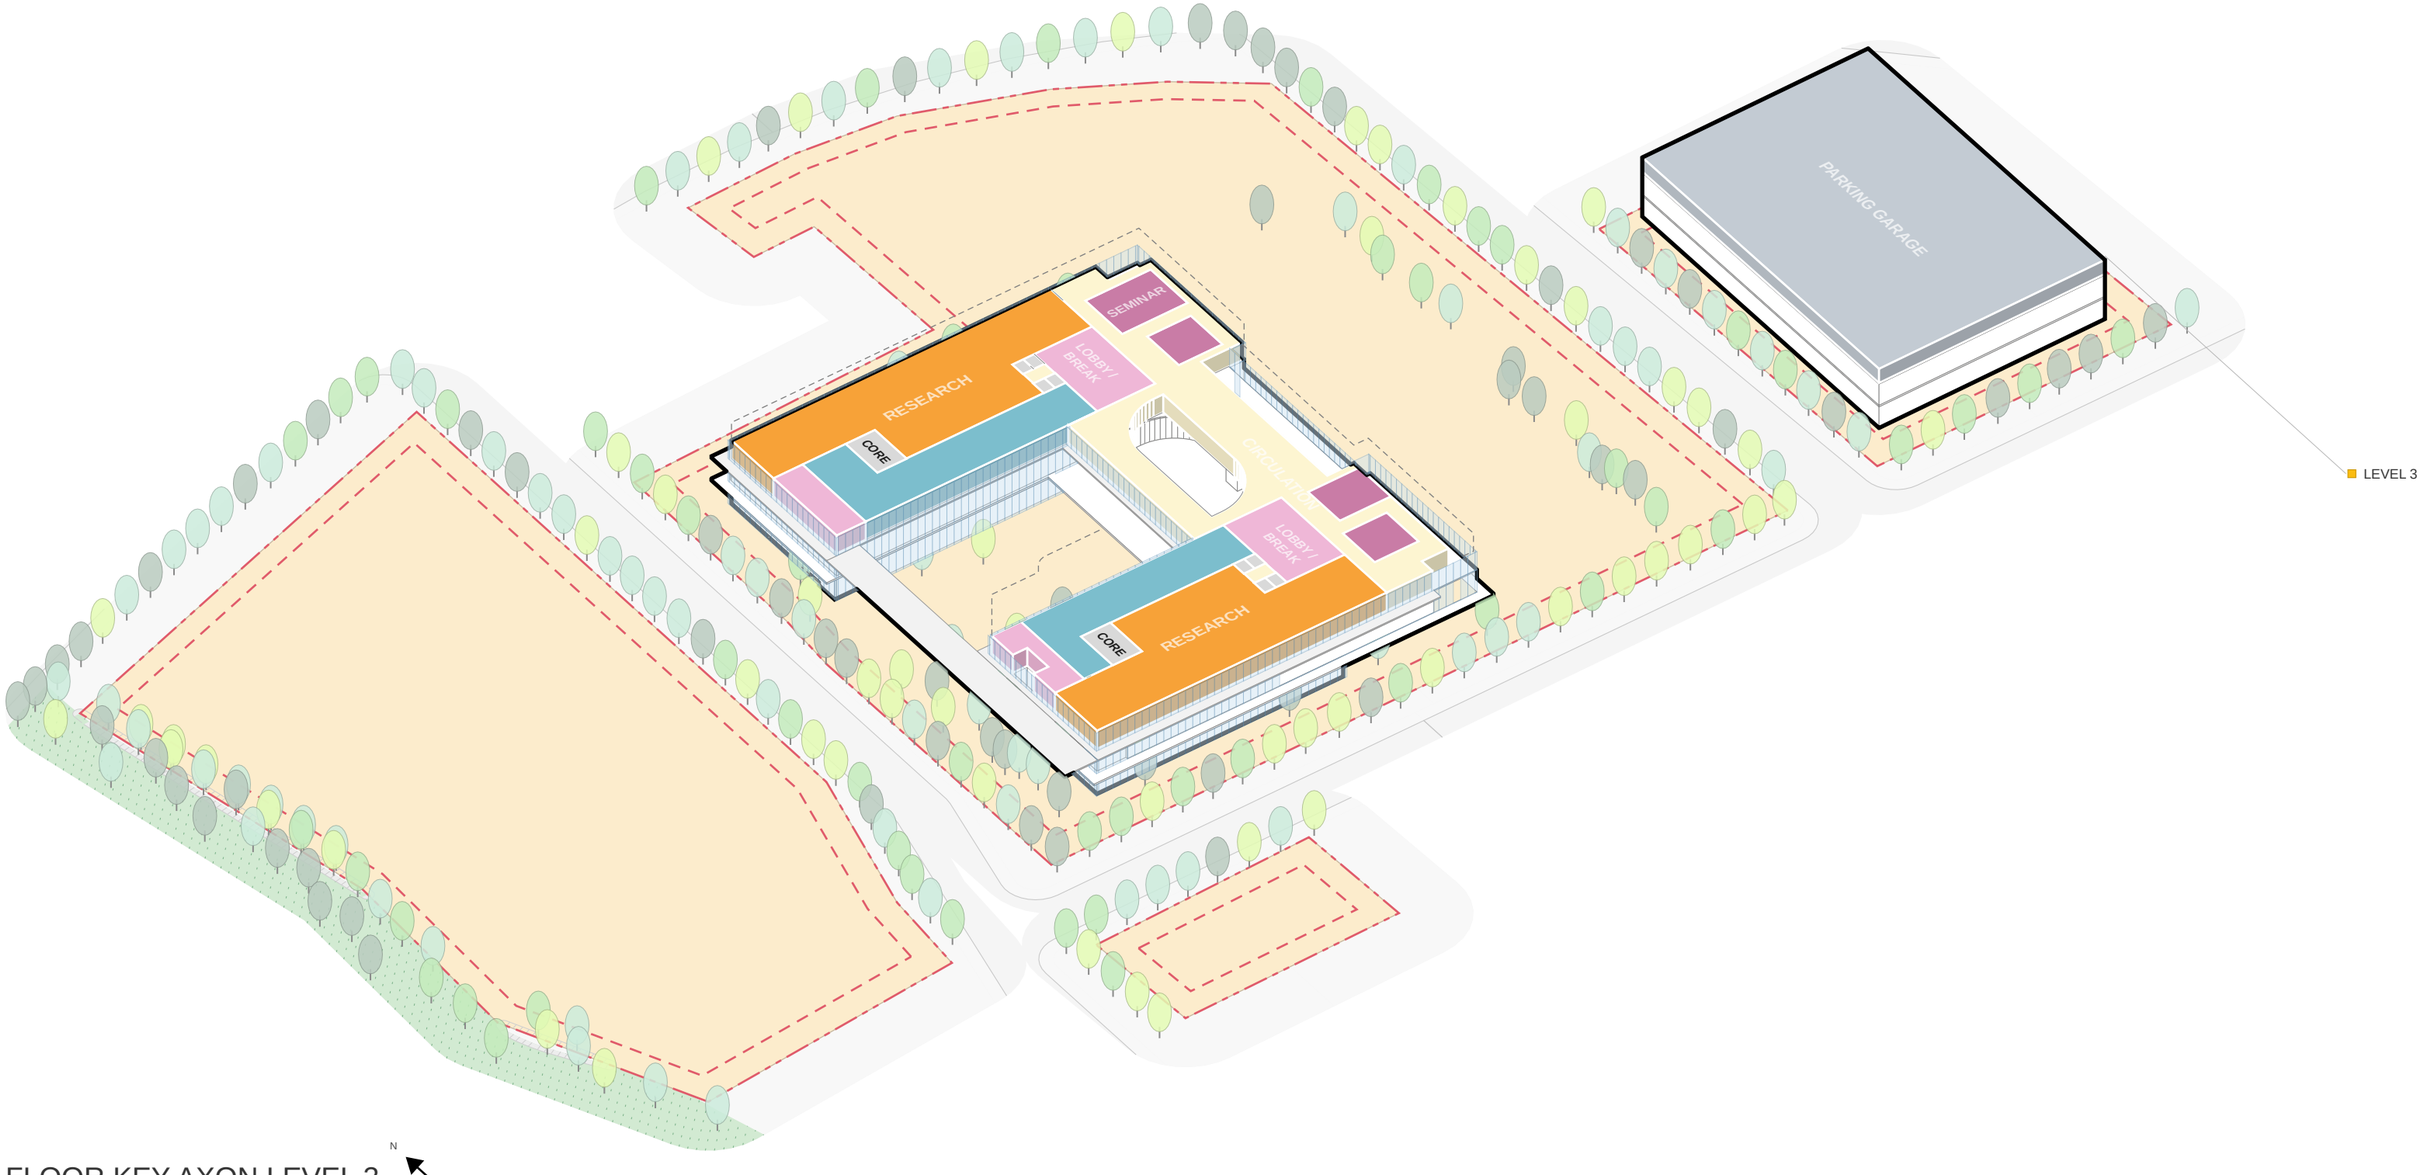

FLOOR KEY AXON LEVEL 3

SCALE 1" = 100'-0"


N

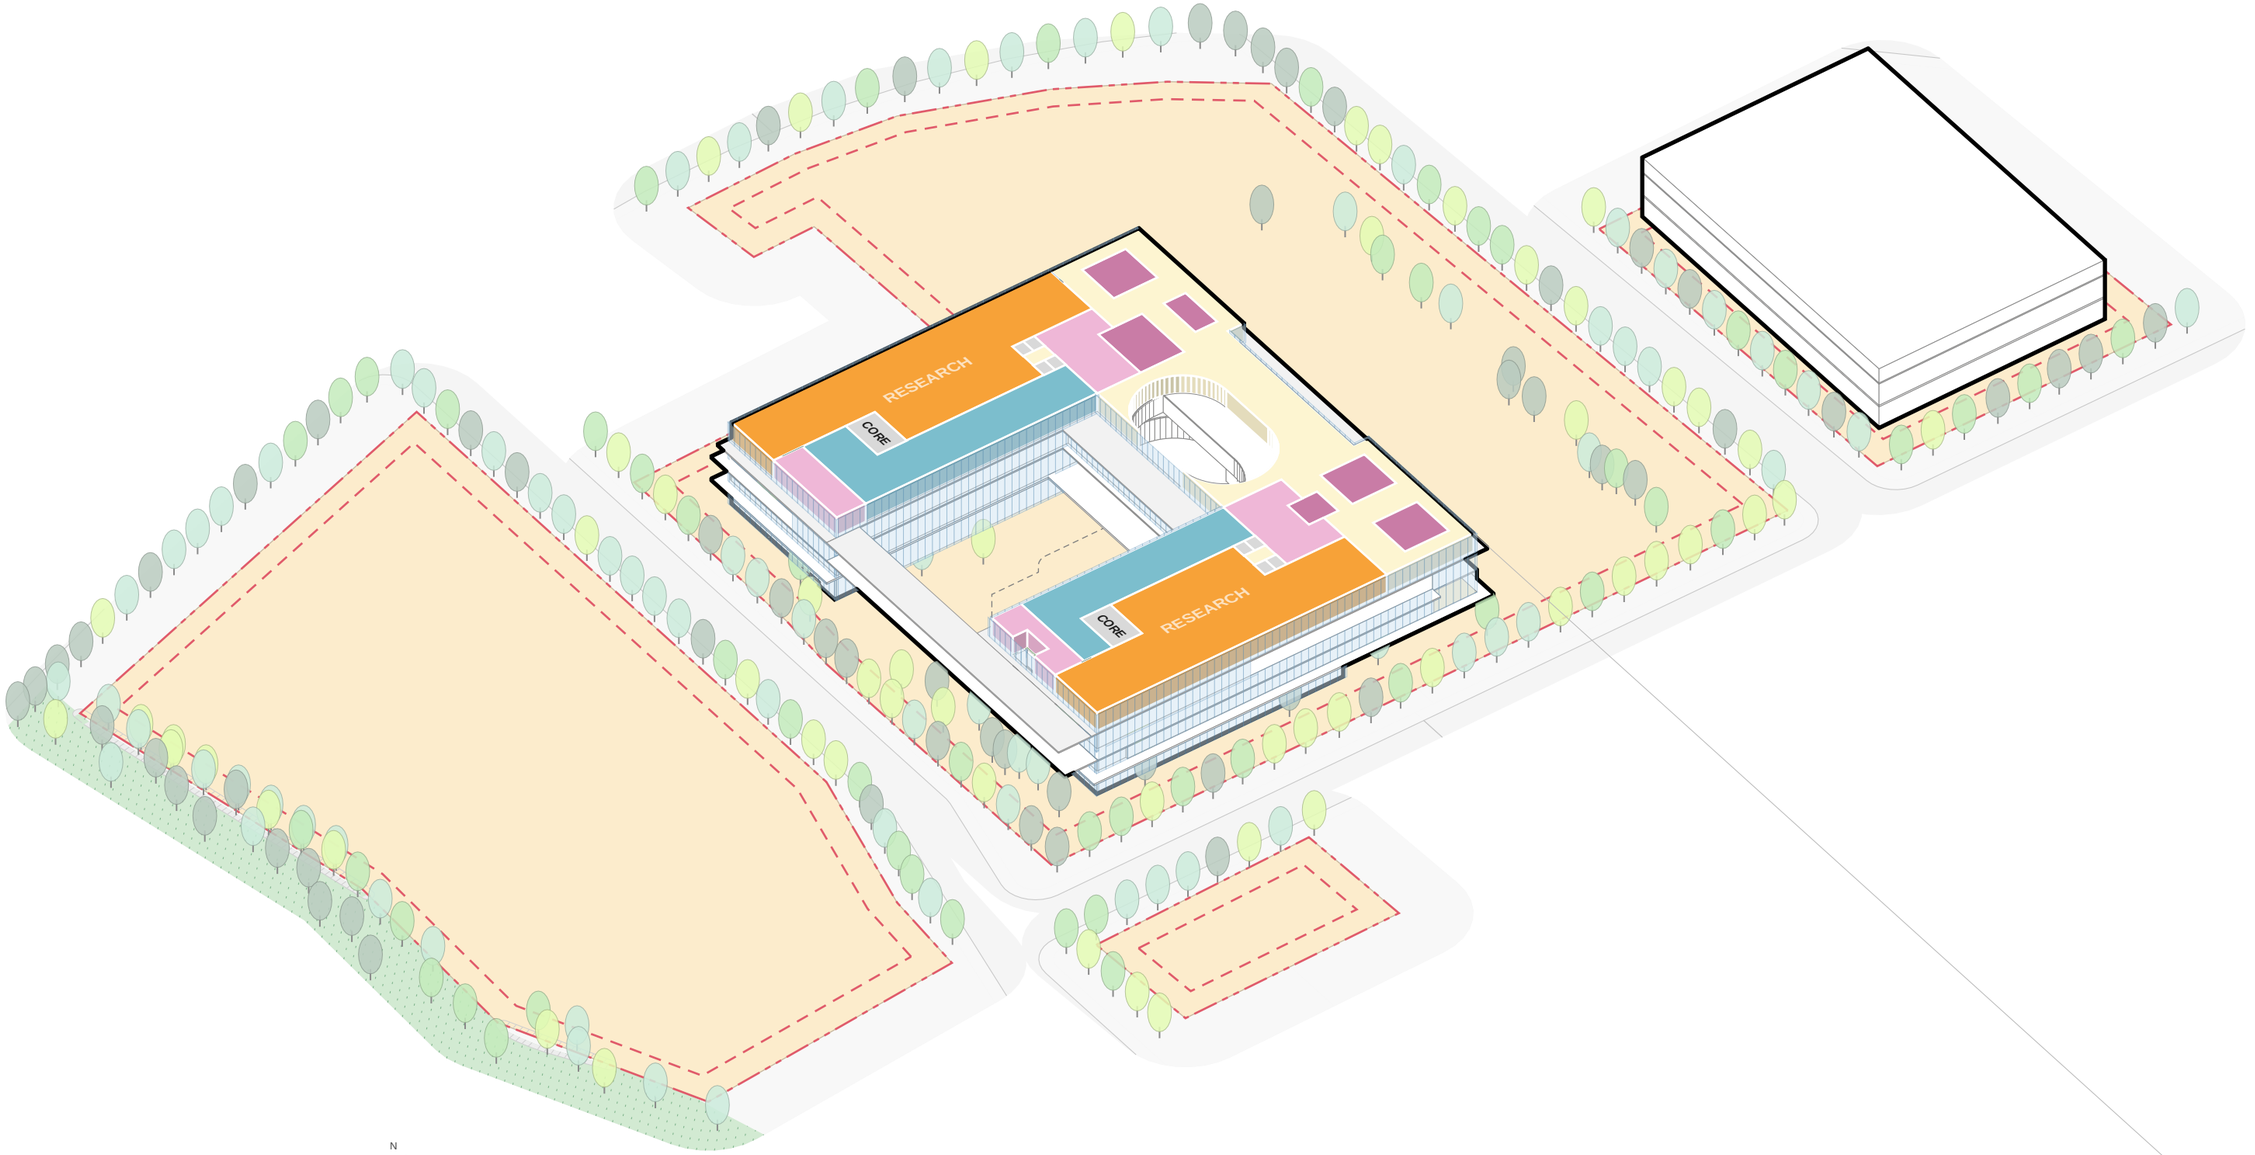

N

FLOOR KEY AXON LEVEL 4


SCALE 1" = 100'-0"

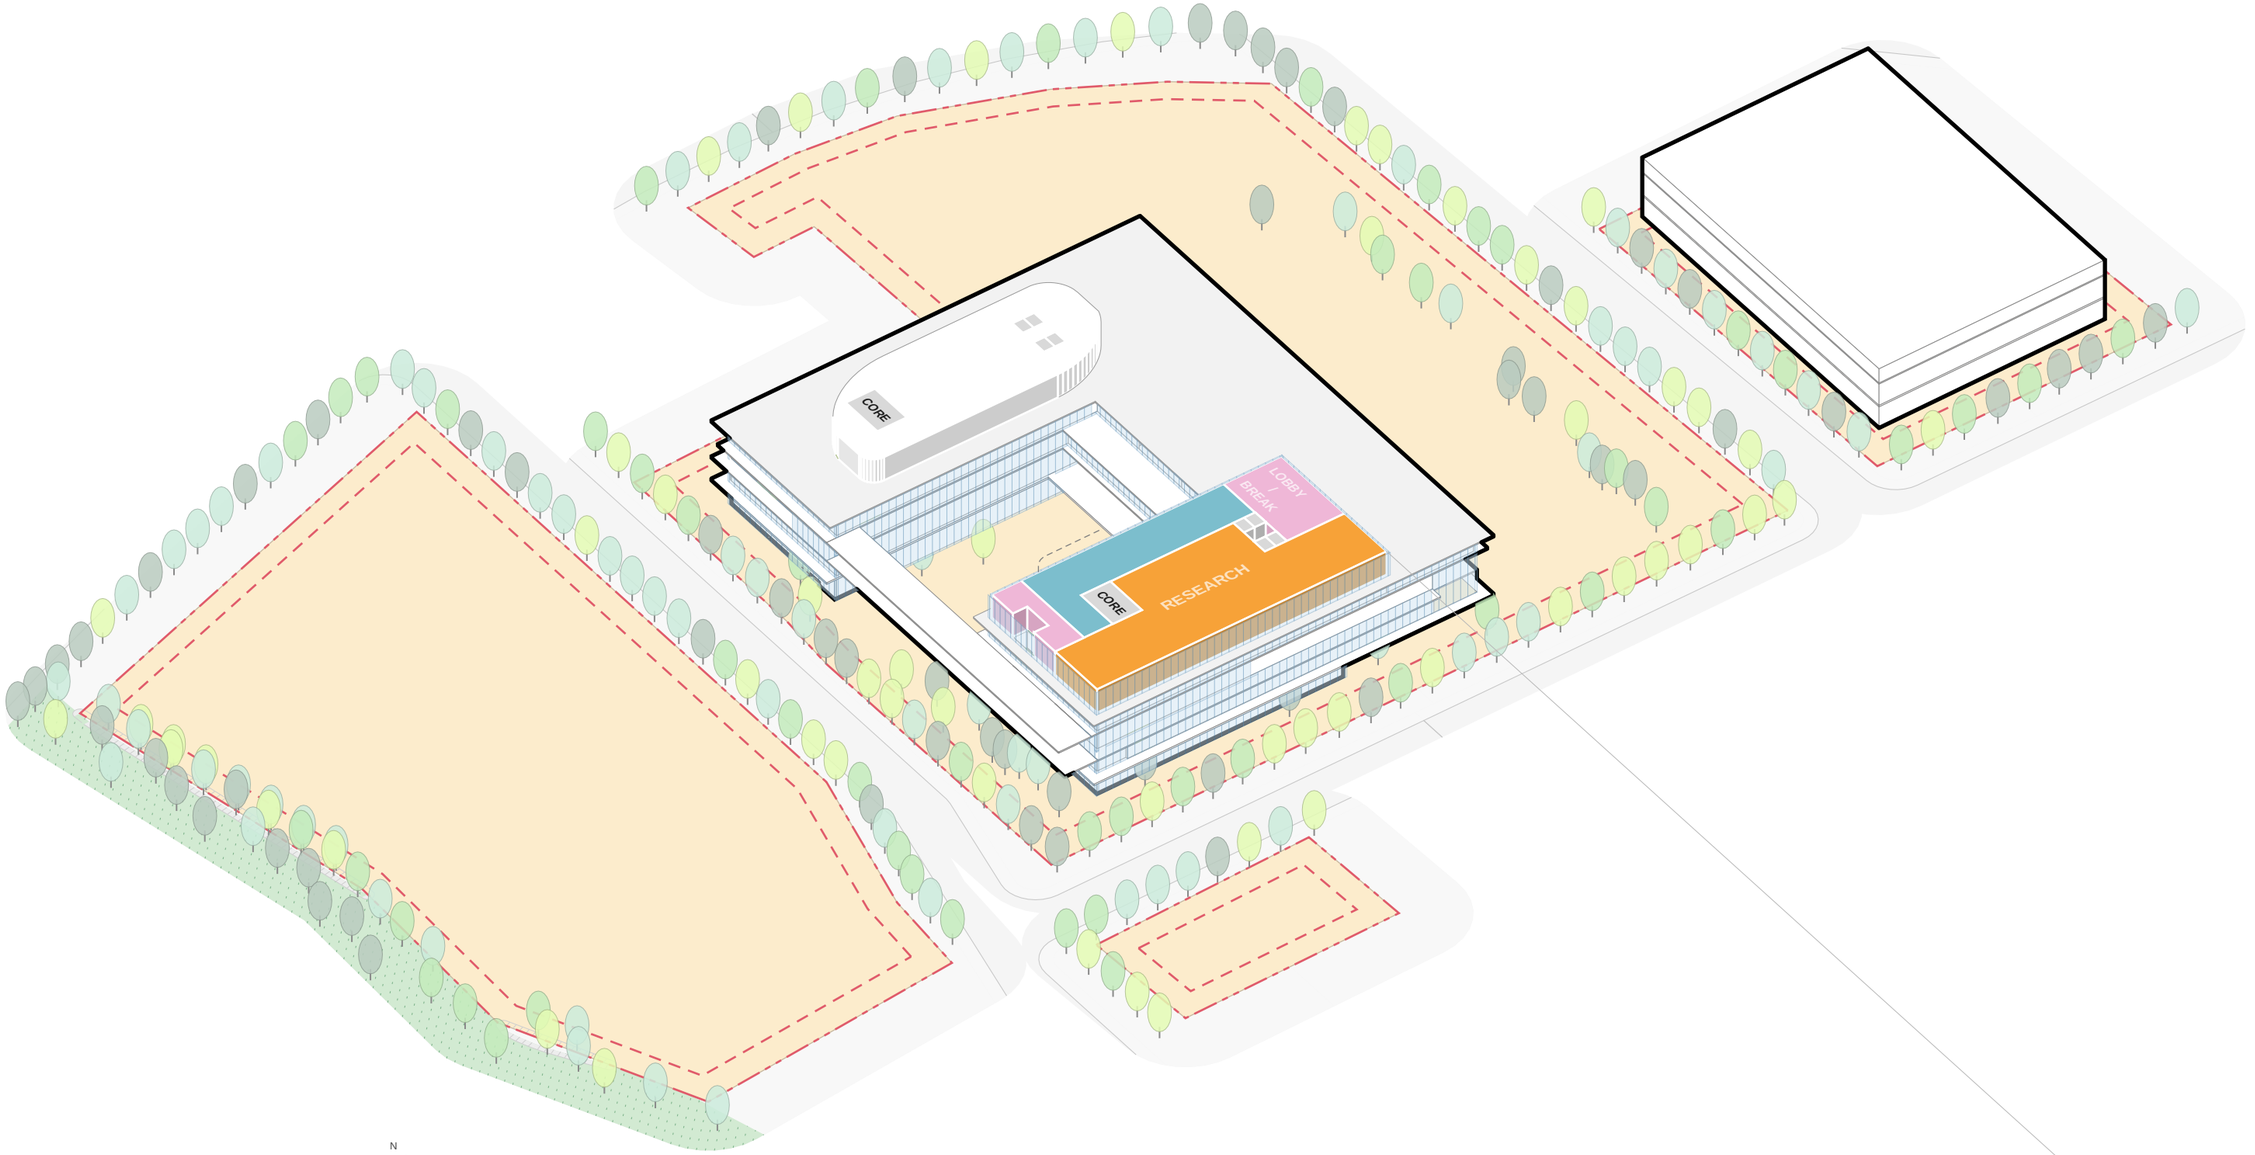

N

FLOOR KEY AXON LEVEL 5

SCALE 1" = 100'-0"

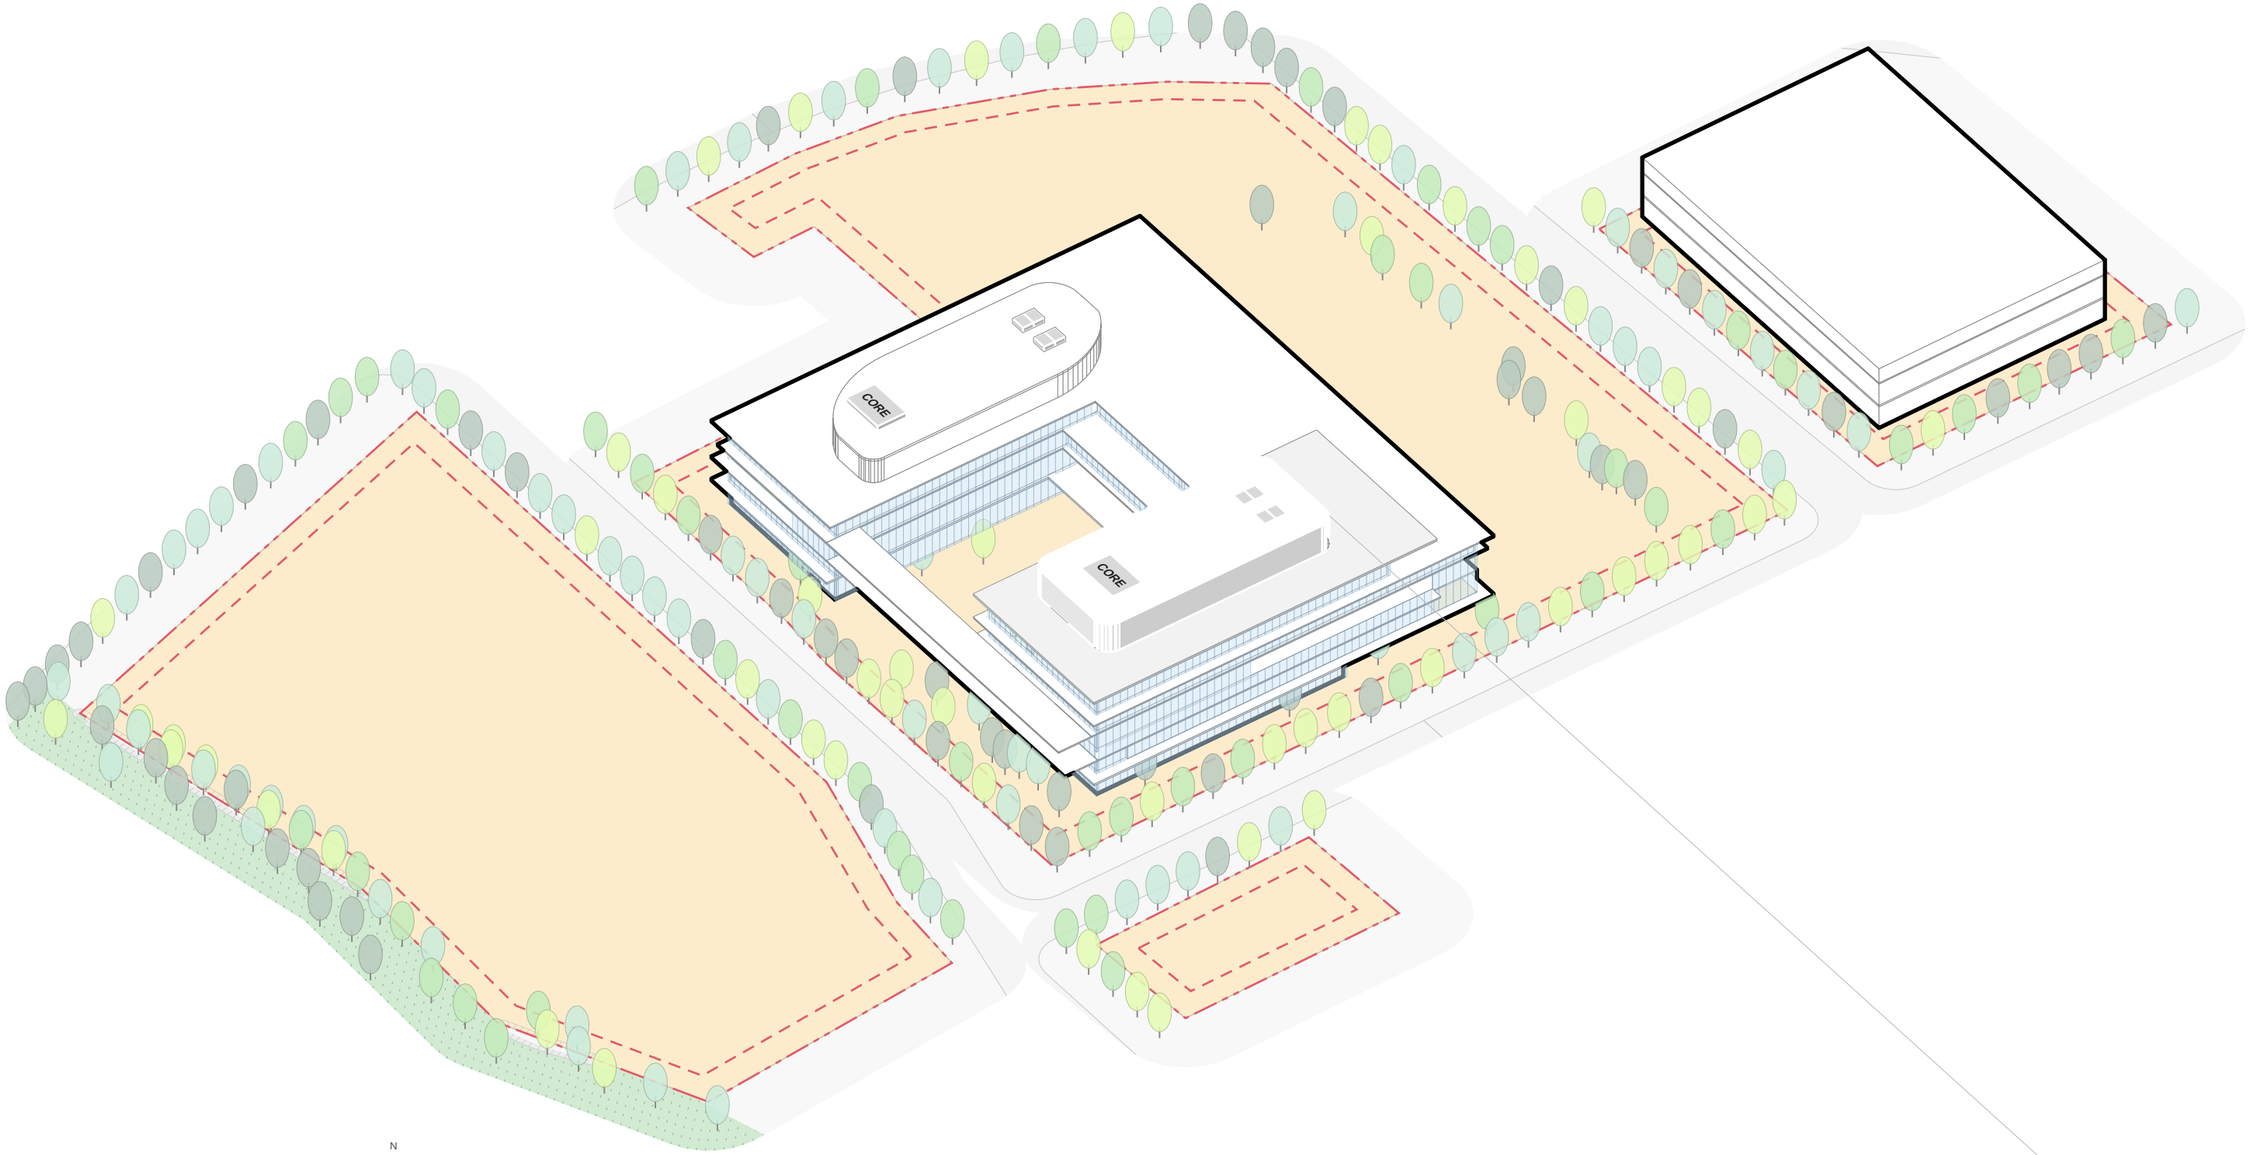

N

FLOOR KEY AXON LEVEL 6

SCALE 1" = 100'-0"

AXON LEGEND



TAG
ROUNDED LABEL + LEADER



PEDESTRIAN FLOW
#E47200 4 PT DASH



VEHICLE FLOW
#6C6C6C 4 PT DASH



TRANSIT STOP
#2F6DB5 ICON



VIEW / GATEWAY
#183C6C 2 PT DASH



SERVICE / LOADING
#6C6C6C ICON + TRIANGLE



ENTRY
#18427E ICON + TRIANGLE



VIEW MARKER
#D8AE78, WHITE NUMBER, LEADER

TREE
CANOPY CIRCLE (PLAN) / LOLLIPOP (AXON)

FUTURE BLDG

FUTURE BUILDING
CONTEXT LABEL: PD CONTEXT LABEL STYLE

MAIN ST

STREET NAME
PD NOTE CAPS, ROTATED ALONG THE STREET

NOTE

NOTE / ANNOTATION
PD NOTE

DETAILED PROGRAM PROPOSAL

CIRCULATION

L1
CIRCULATION

L2
CIRCULATION

L3
CIRCULATION

L4
CIRCULATION


103,461 GSF

CORE


L1
CORE




L2
CORE

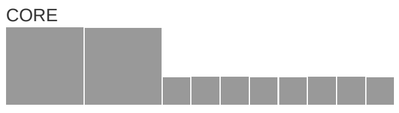


L3
CORE

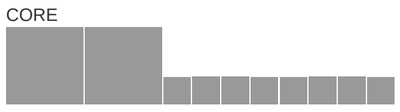

L4
CORE

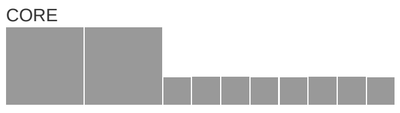

L5
CORE

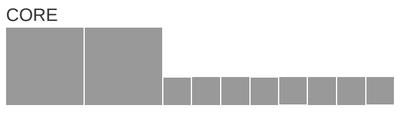

L6
CORE



15,776 GSF

LAB

L1
CORE LABS



QUANTUM HIGH MIP



PROTOTYPING / FABRICATION



L2
PARTNER / INCUBATOR



RESEARCH



L3
RESEARCH



L4
RESEARCH



L5
RESEARCH



123,631 GSF

BUILDING SUPPORT / MECHANICAL / STORAGE

L1
MEP SUPPORT

SECURITY

BUILDING SUPPORT / MECHANICAL / STORAGE

LOADING DOCK

STORAGE

14,615 GSF

CONFERENCE


L1
COMBINABLE CLASSROOMS



L2
CONFERENCE




L3
CONFERENCE

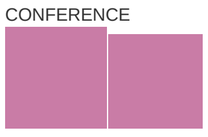

SEMINAR



L4
EXECUTIVE BRIEFING

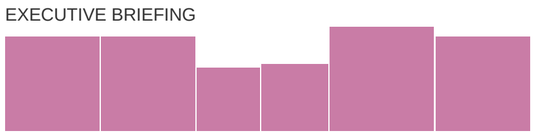

18,049 GSF


LOBBY / BREAK

L1
COFFEE KIOSK




FITNESS

L2
LOBBY / BREAK

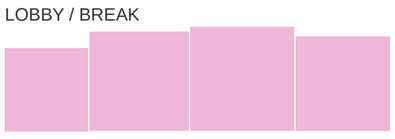


DINING PREP

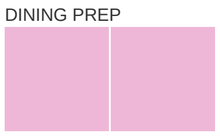


L3
LOBBY / BREAK



L4
LOBBY / BREAK

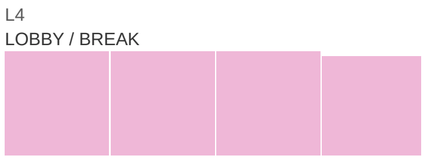

L5
LOBBY / BREAK

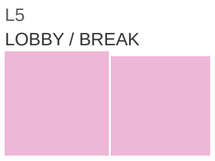

43,766 GSF

ASSEMBLY / AUDITORIUM / BOARDROOM

L1
AUDITORIUM



5,302 GSF

PARKING

L1
PARKING GARAGE



L2
PARKING GARAGE



L3
PARKING GARAGE



151,191 GSF

OFFICE

L2
OFFICE



L3
OFFICE



L4
OFFICE




L5
OFFICE




47,515 GSF

SHELL / PENTHOUSE

L5
SHELL / PENTHOUSE

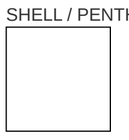


L6
SHELL / PENTHOUSE

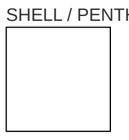

29,855 GSF

MODEL (GSF) — TOTAL 553,161 GSF

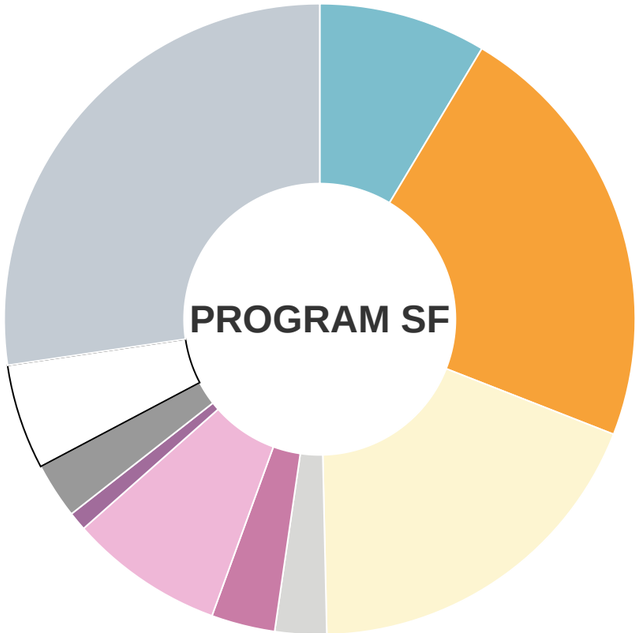


TOTAL: 553,161 GSF

- OFFICE 47,515 SF
- LAB 123,631 SF
- CIRCULATION 103,461 SF
- BUILDING SUPPORT / MECHANICAL / STORAGE 14,615 SF
- CONFERENCE 18,049 SF
- LOBBY / BREAK 43,766 SF
- ASSEMBLY / AUDITORIUM / BOARDROOM 5,302 SF
- CORE 15,776 SF
- SHELL / PENTHOUSE 29,855 SF
- PARKING 151,191 SF

PROGRAM DEVELOPMENT SUMMARY


553,161 GSF



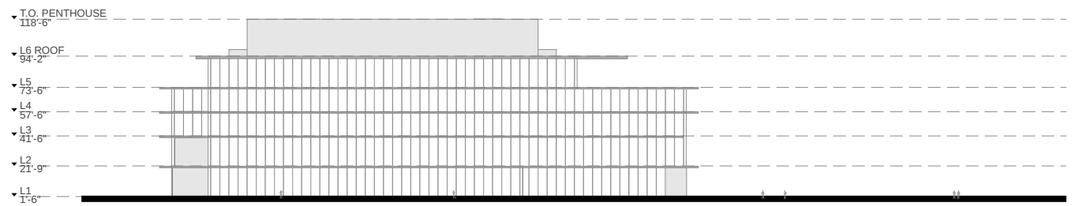

ELEVATION E1

SCALE 1" = 100'-0"

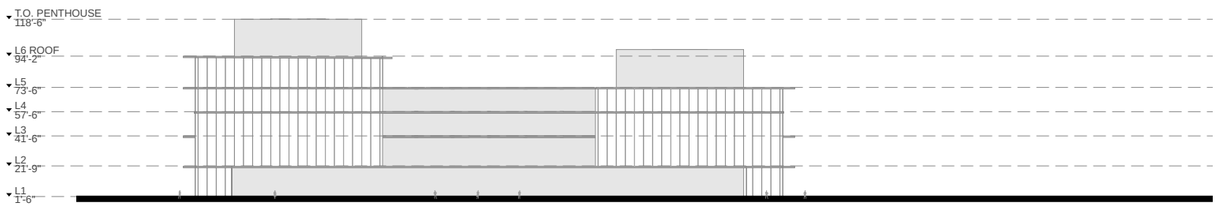

ELEVATION E2

SCALE 1" = 100'-0"